CLASSE TAVOLA 9

ASSONOMETRIA ISOMETRICA DI UN EDIFICIO CON CAMPANILE

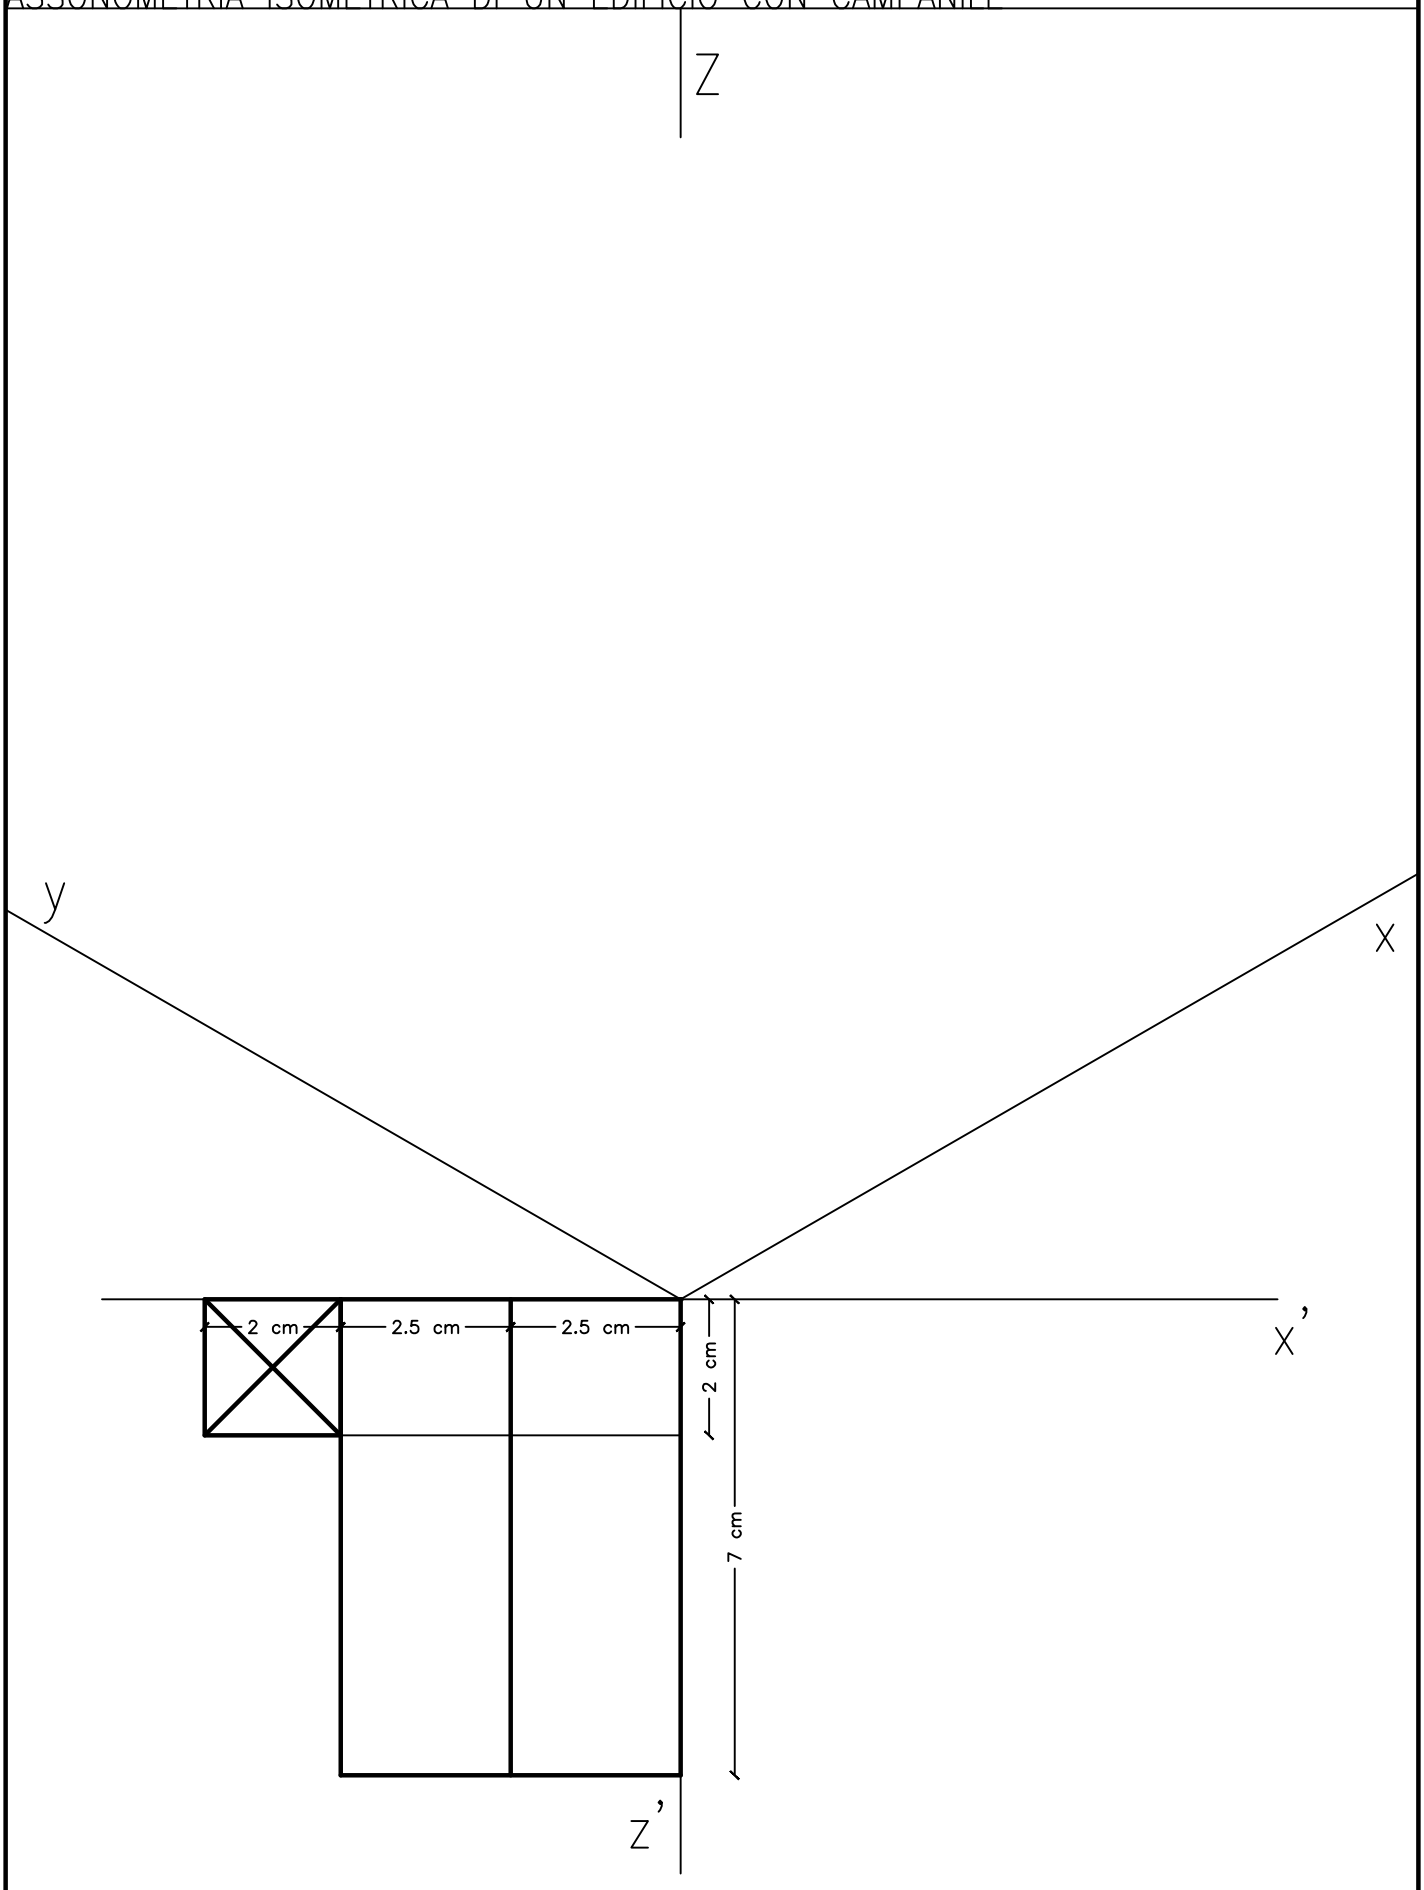

DATA ALUNNO

CLASSE TAVOLA 9

ASSONOMETRIA ISOMETRICA DI UN EDIFICIO CON CAMPANILE

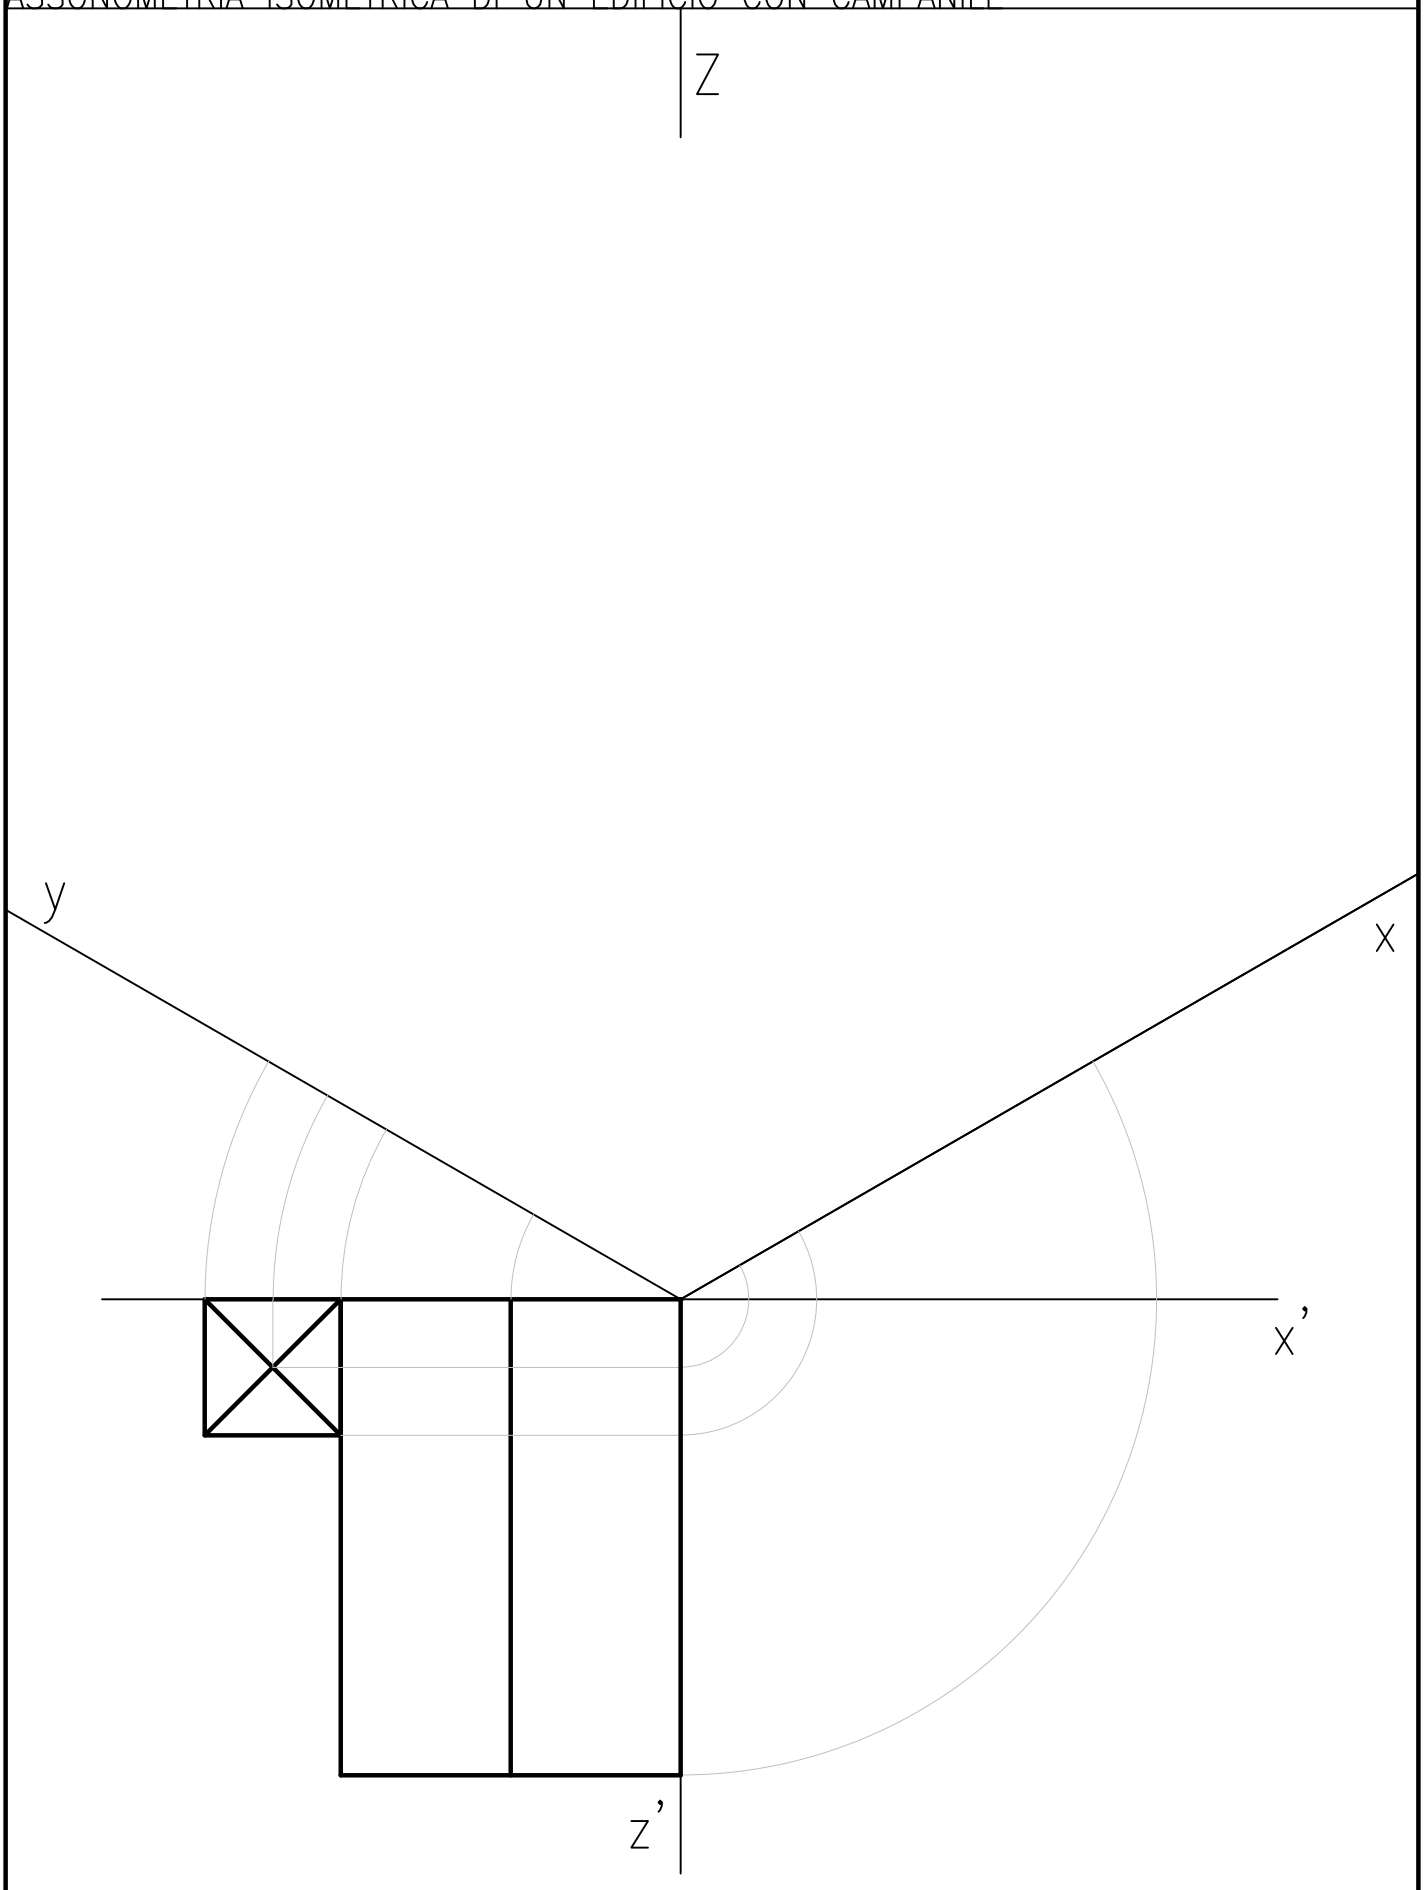

DATA ALUNNO

CLASSE TAVOLA 9

ASSONOMETRIA ISOMETRICA DI UN EDIFICIO CON CAMPANILE

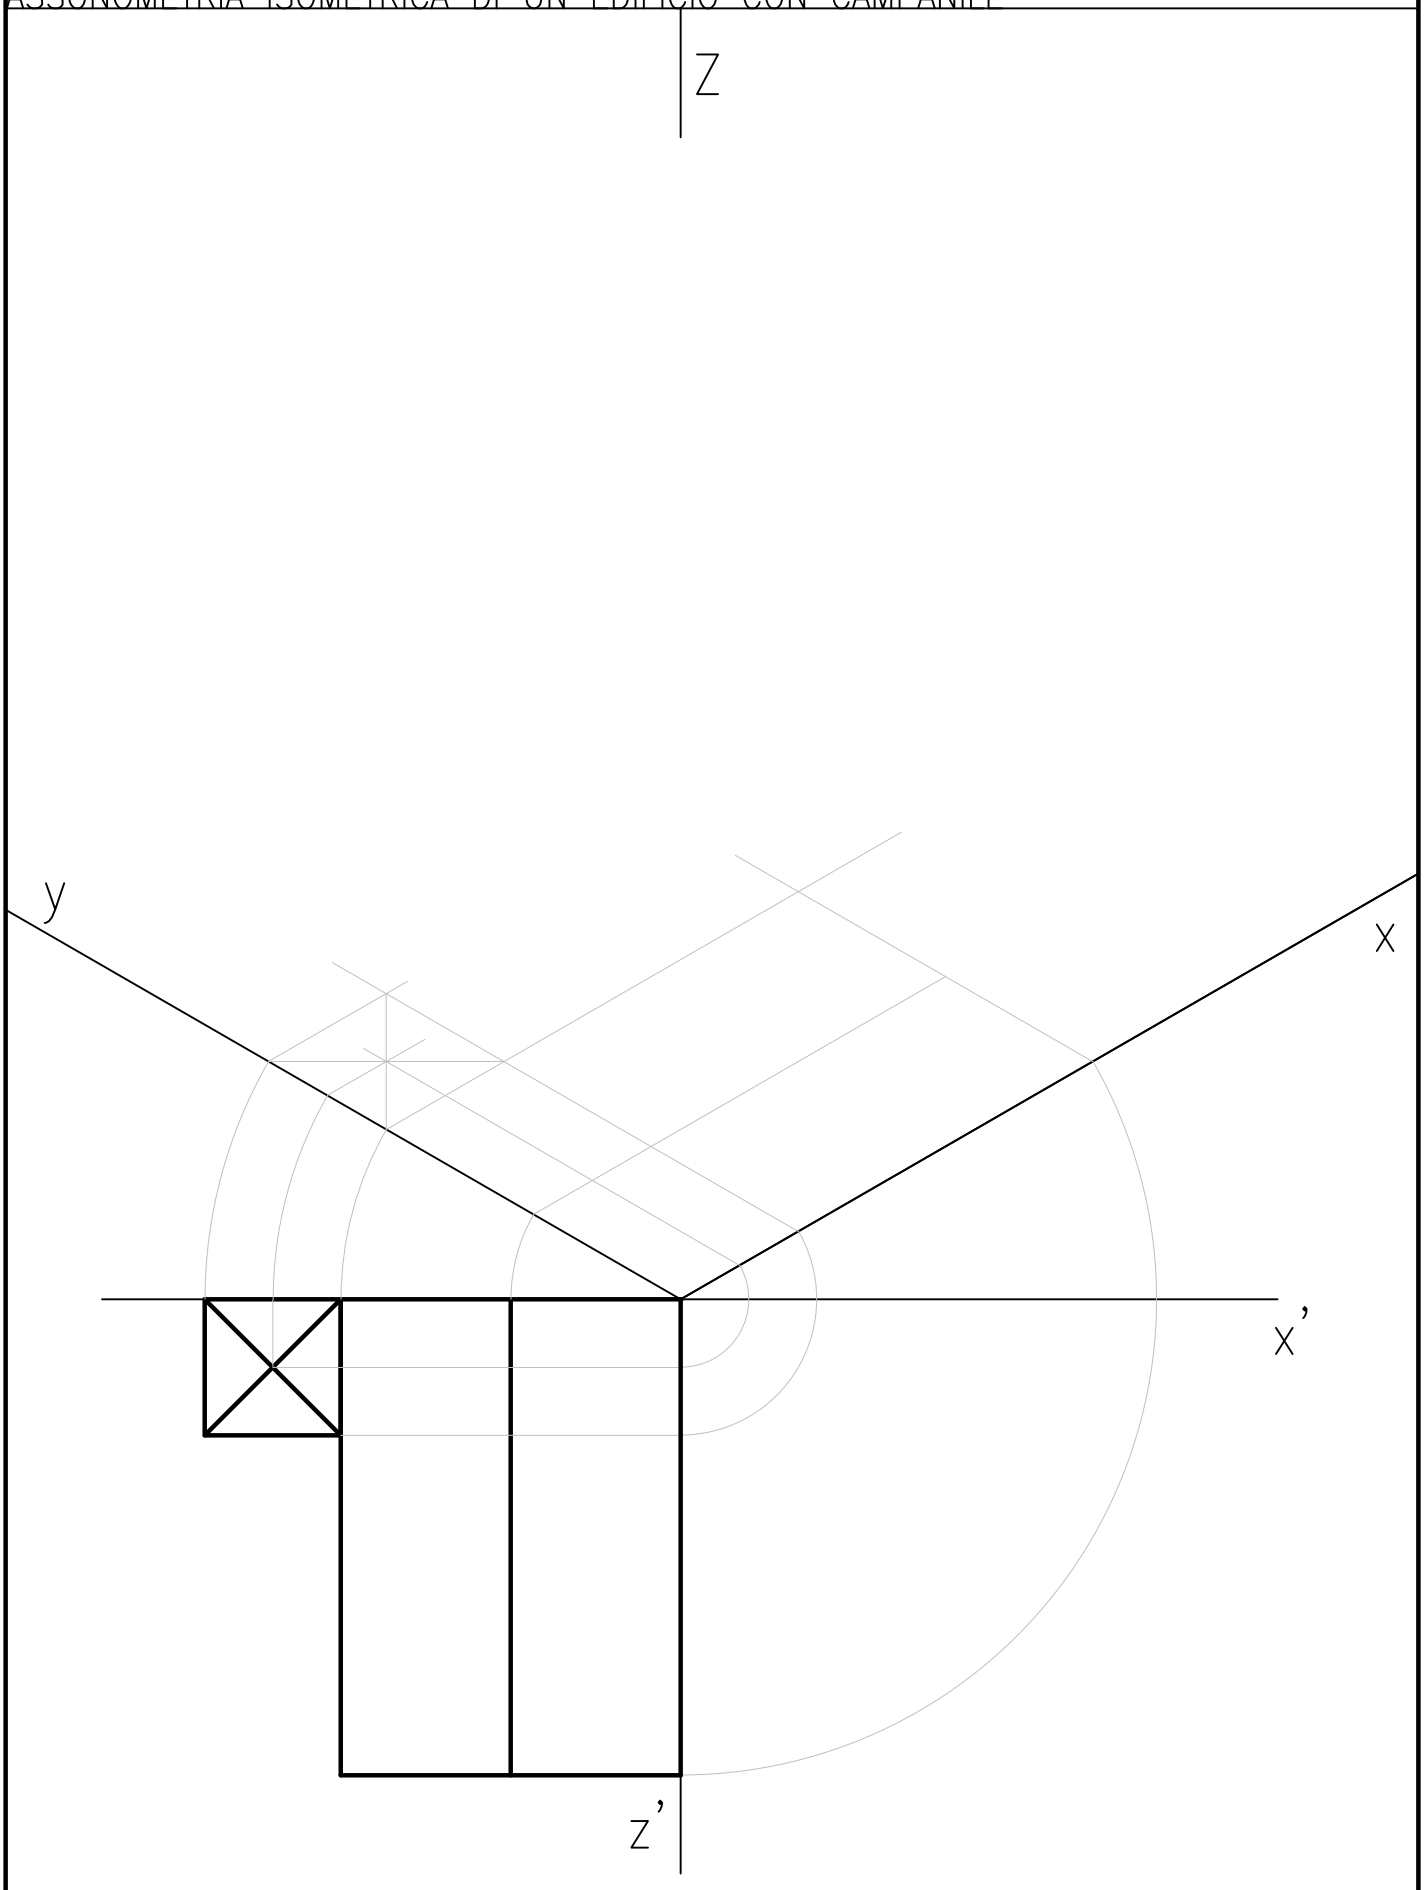

DATA ALUNNO

CLASSE TAVOLA 9

ASSONOMETRIA ISOMETRICA DI UN EDIFICIO CON CAMPANILE

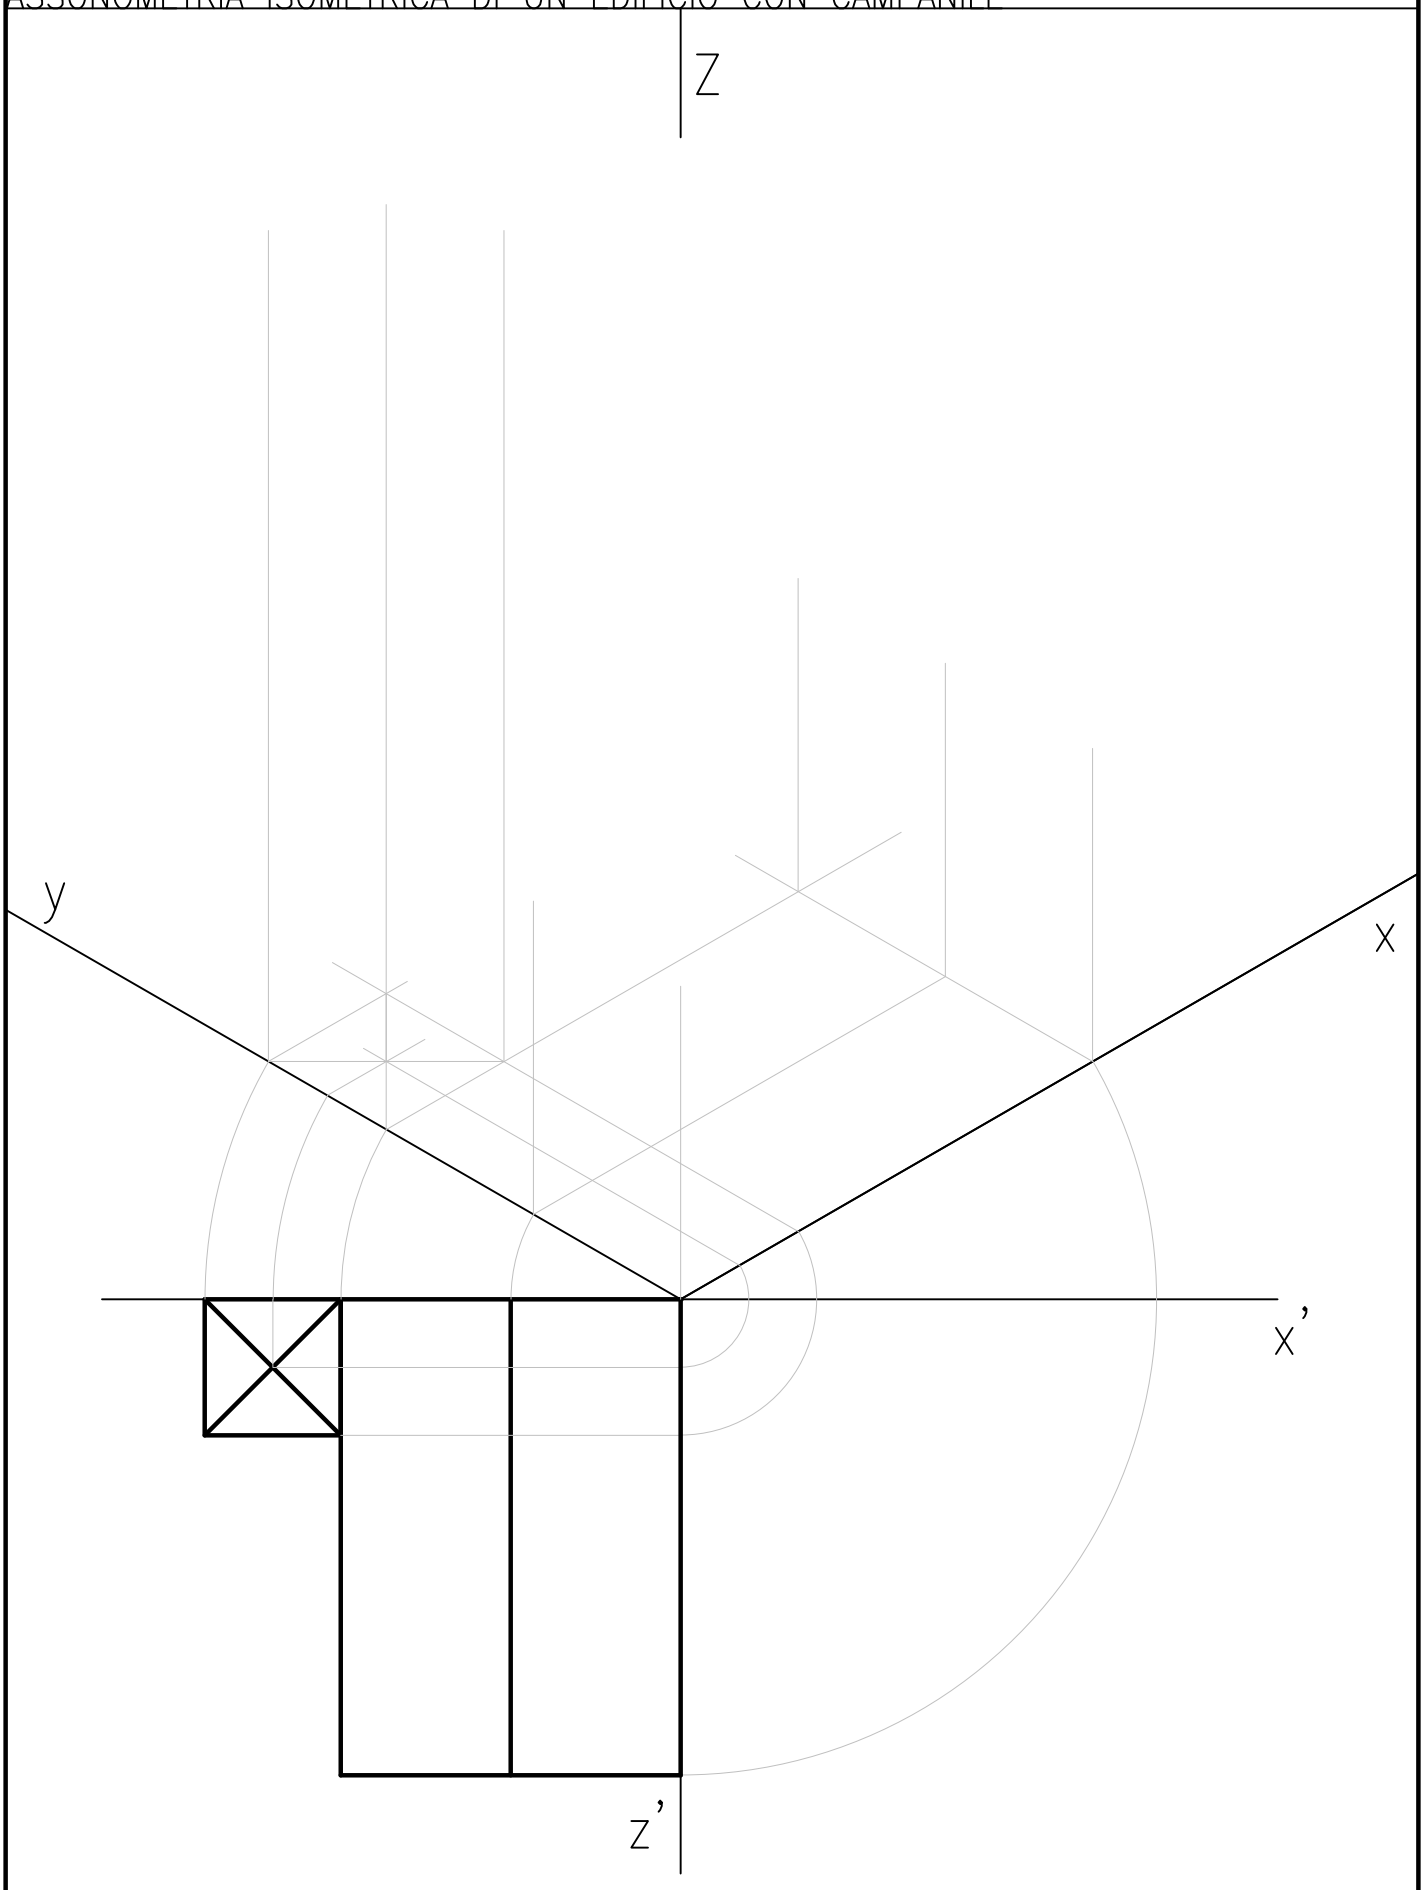

DATA ALUNNO

CLASSE TAVOLA 9

ASSONOMETRIA ISOMETRICA DI UN EDIFICIO CON CAMPANILE

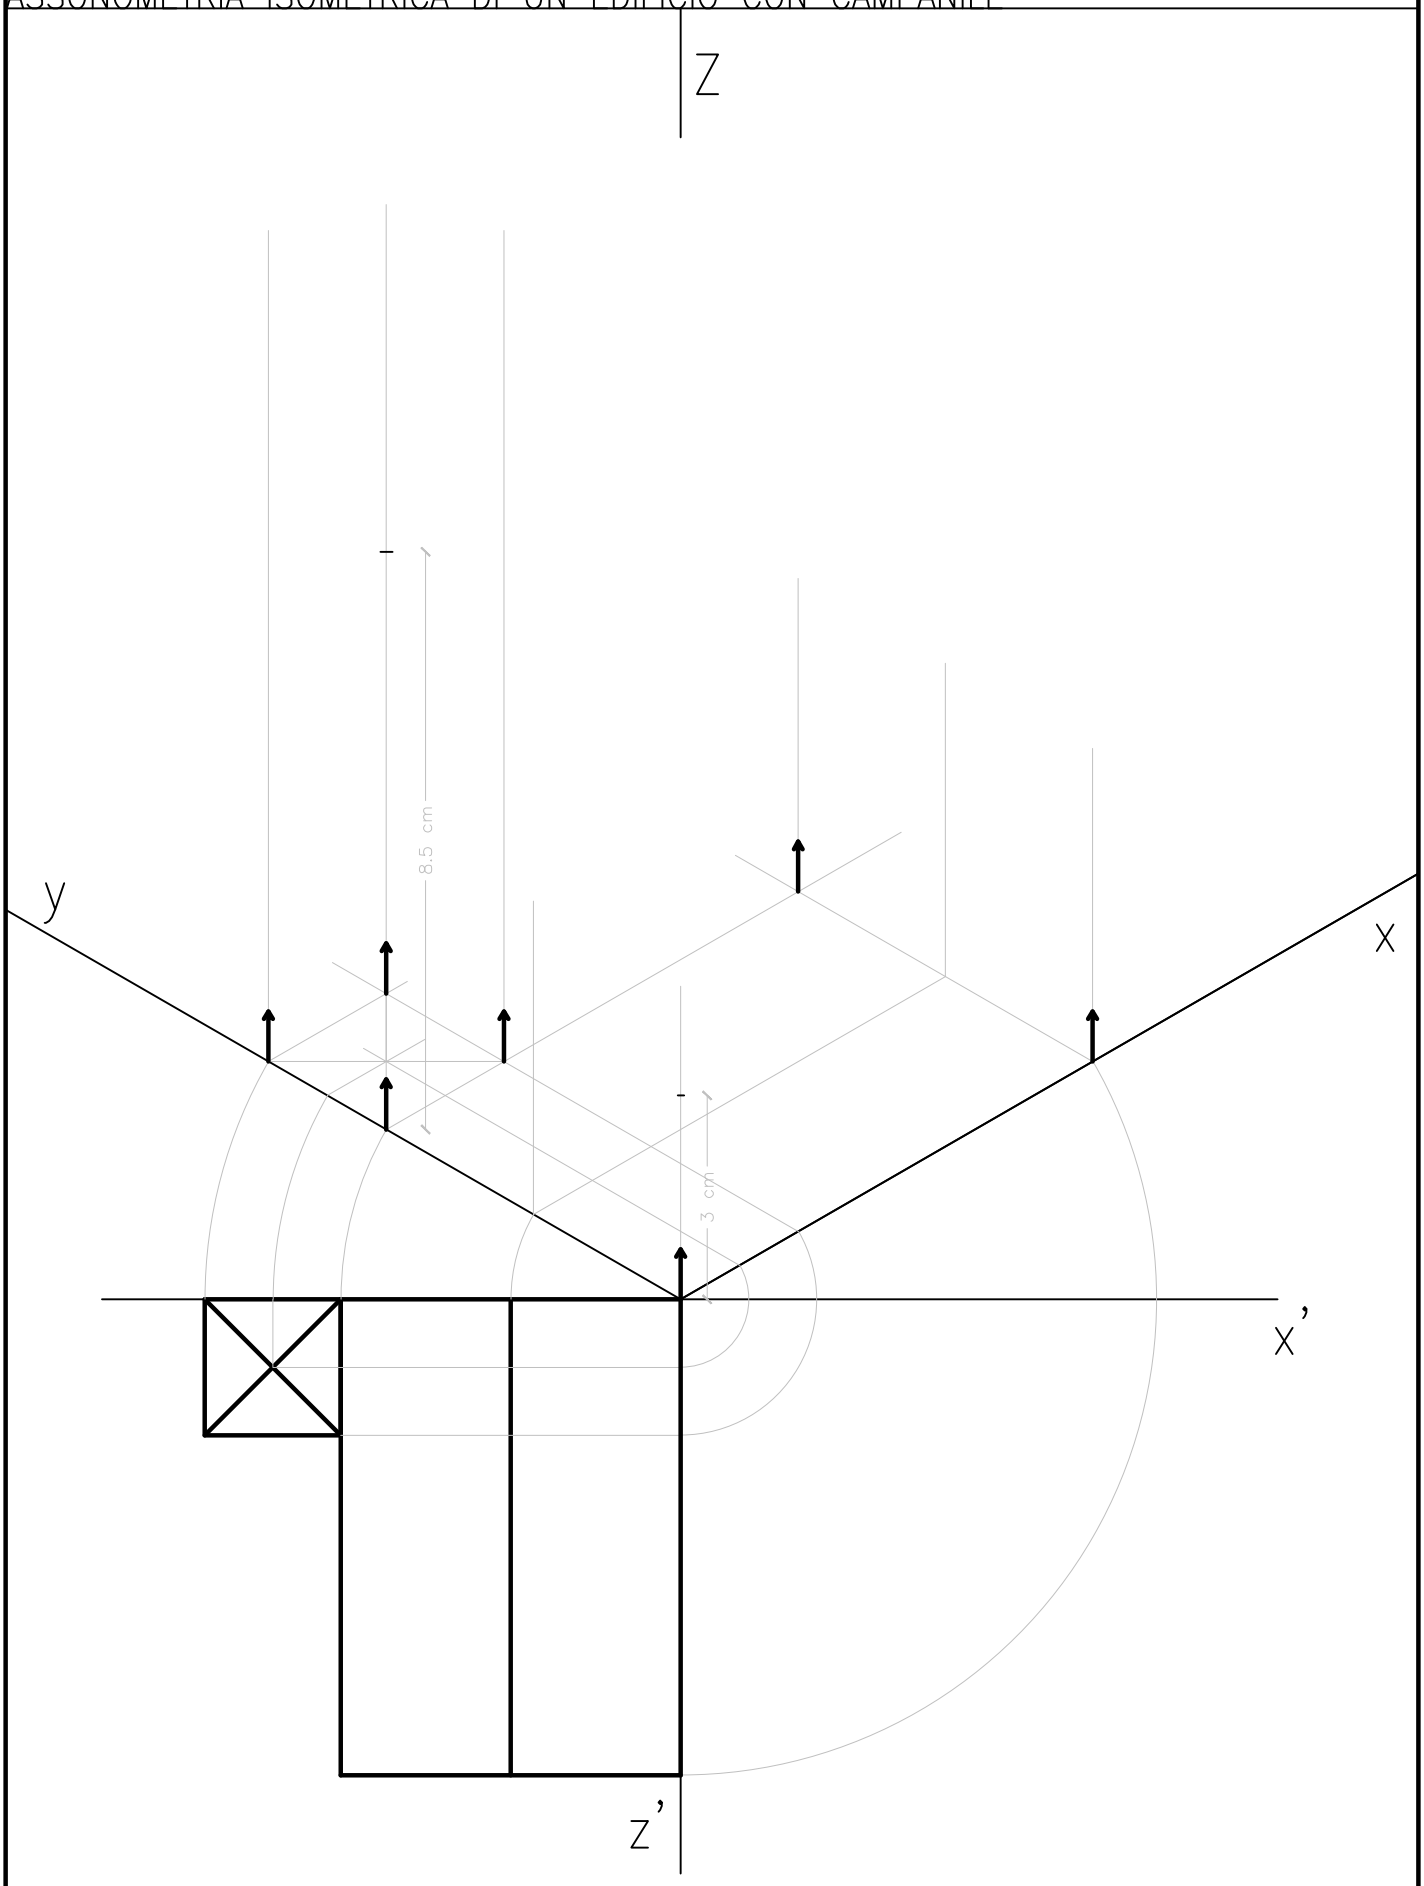

DATA ALUNNO

CLASSE TAVOLA 9

ASSONOMETRIA ISOMETRICA DI UN EDIFICIO CON CAMPANILE

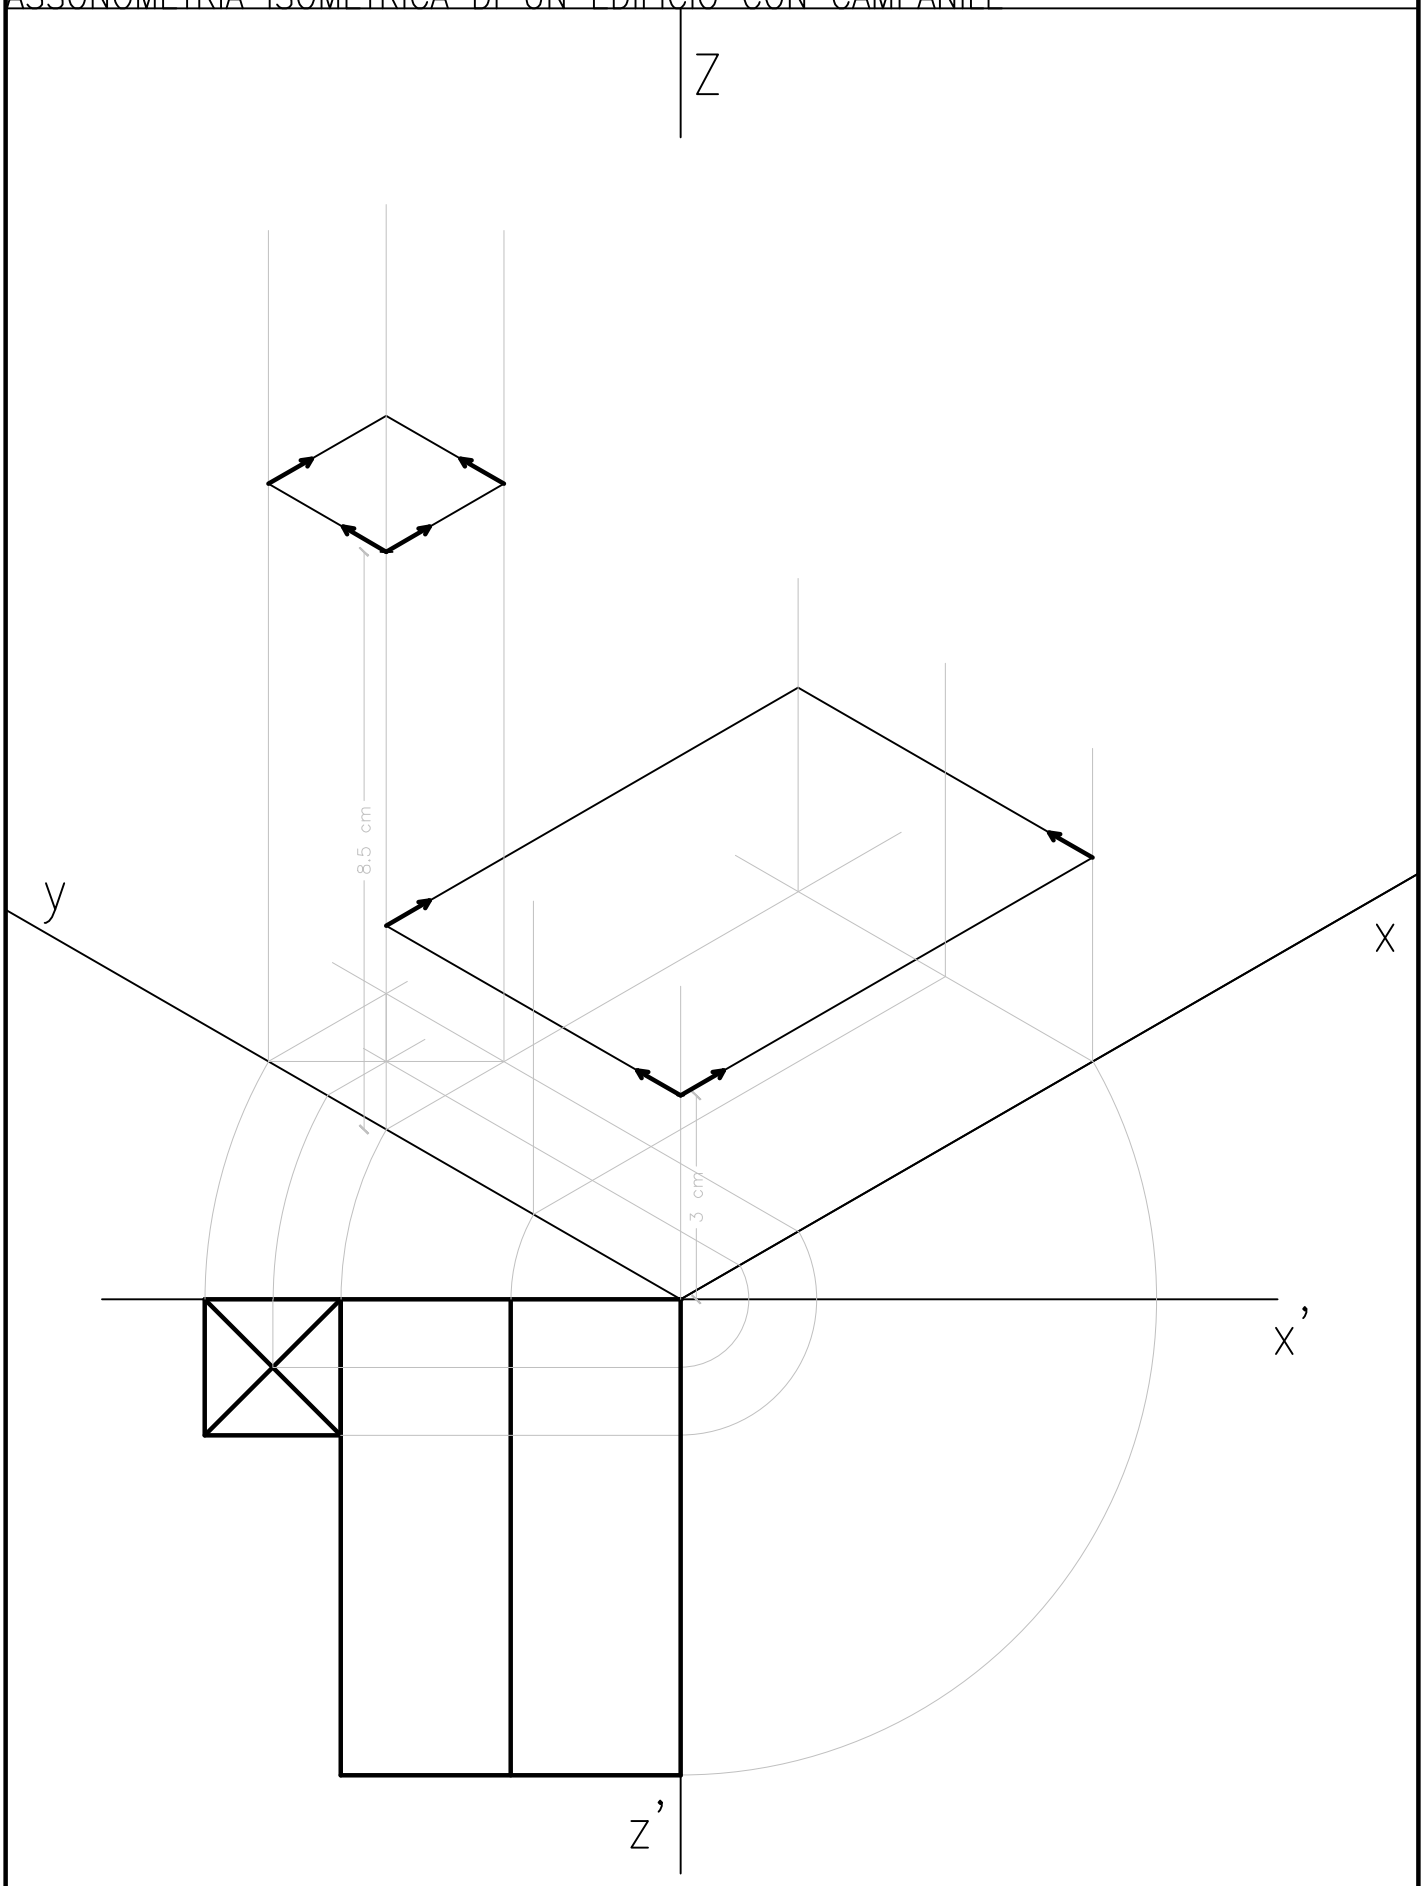

DATA ALUNNO

CLASSE TAVOLA 9

ASSONOMETRIA ISOMETRICA DI UN EDIFICIO CON CAMPANILE

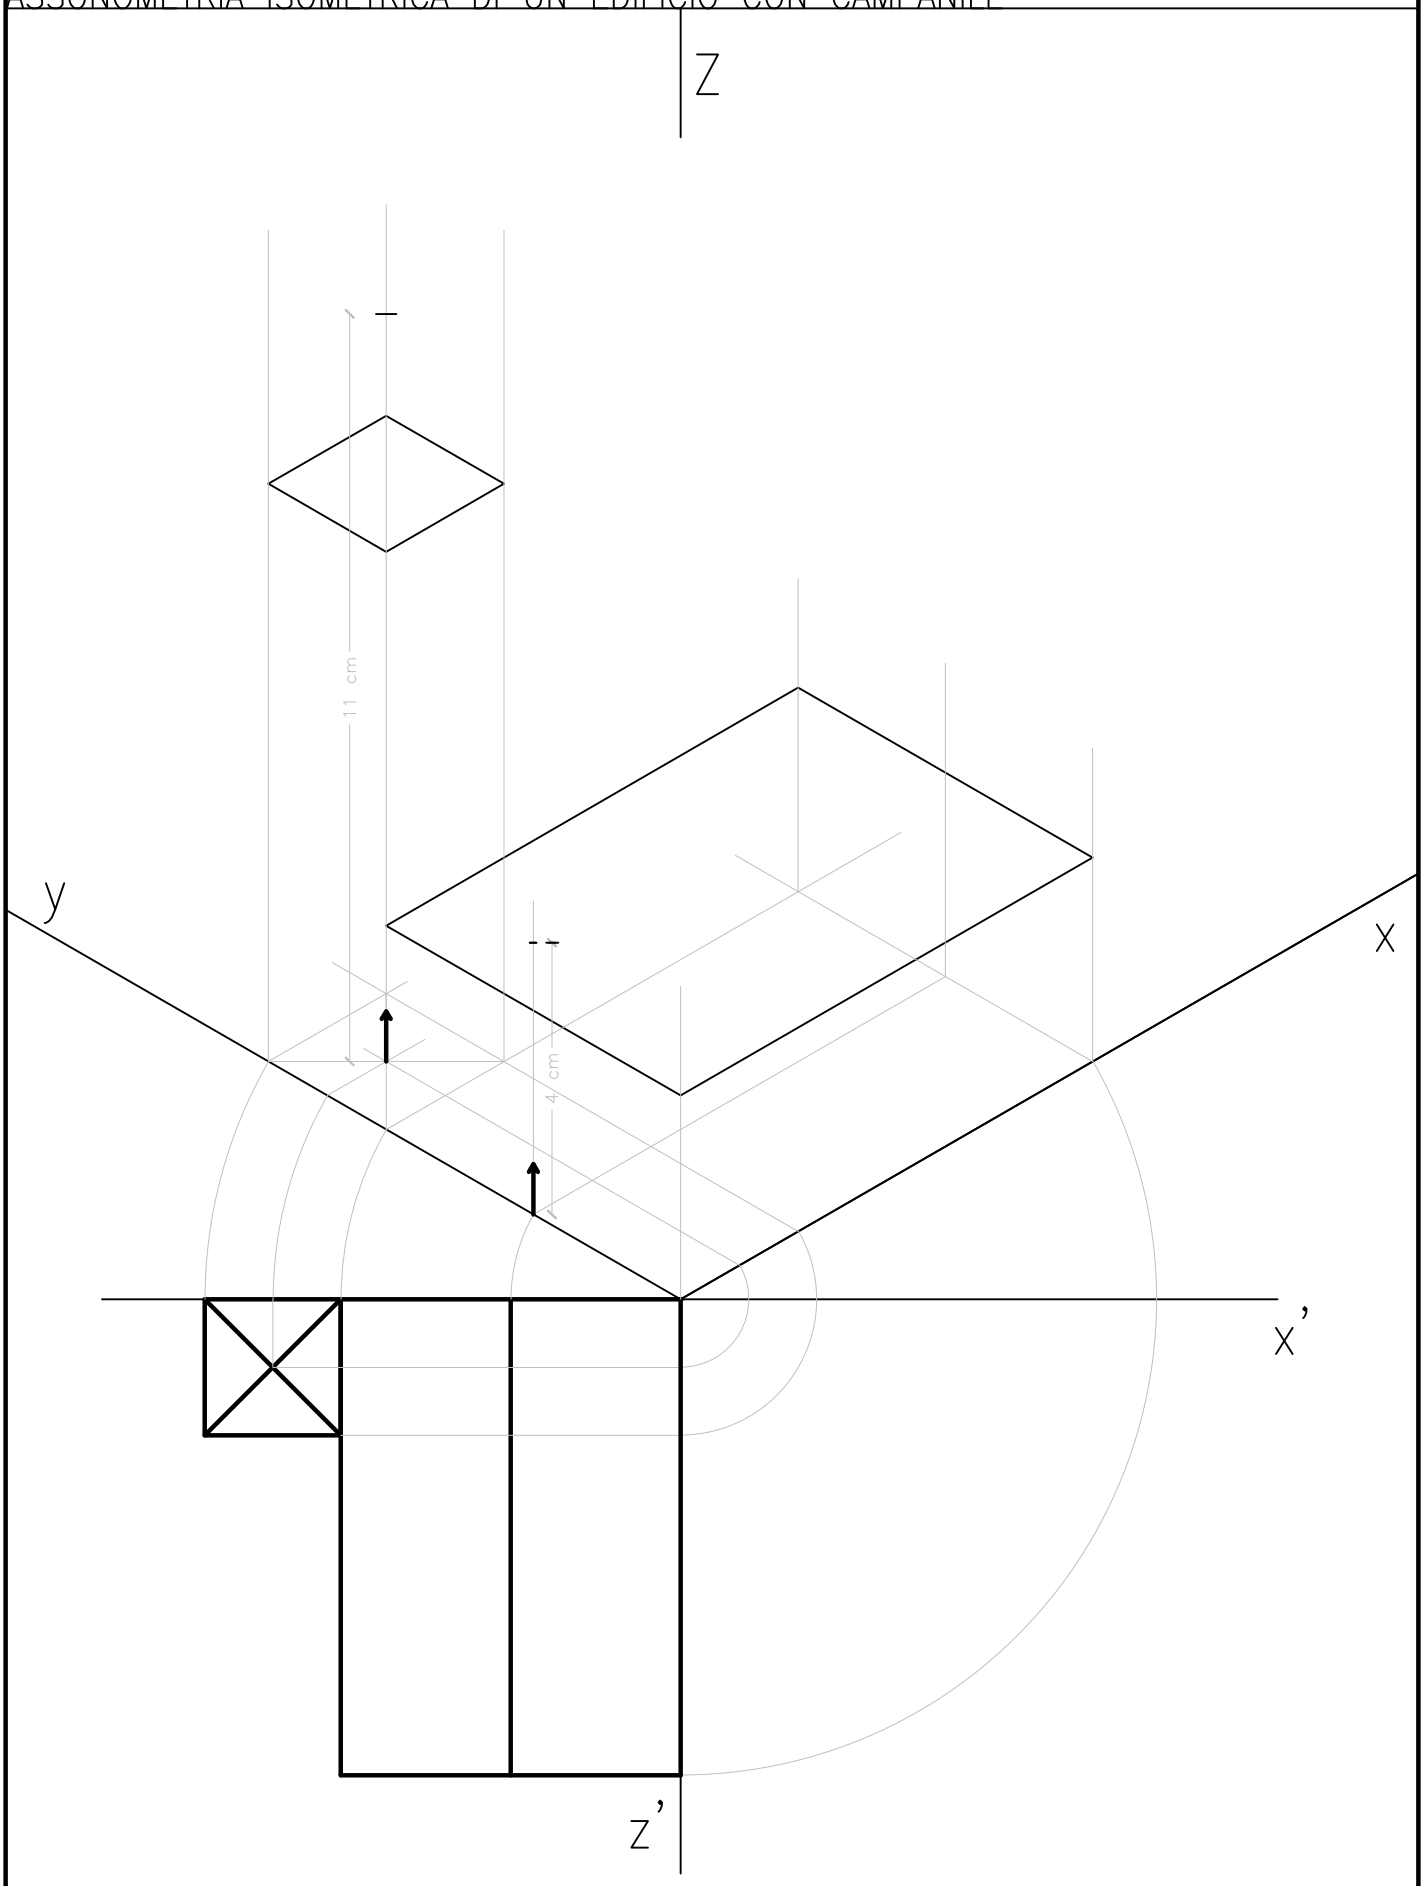

DATA ALUNNO

CLASSE TAVOLA 9

ASSONOMETRIA ISOMETRICA DI UN EDIFICIO CON CAMPANILE

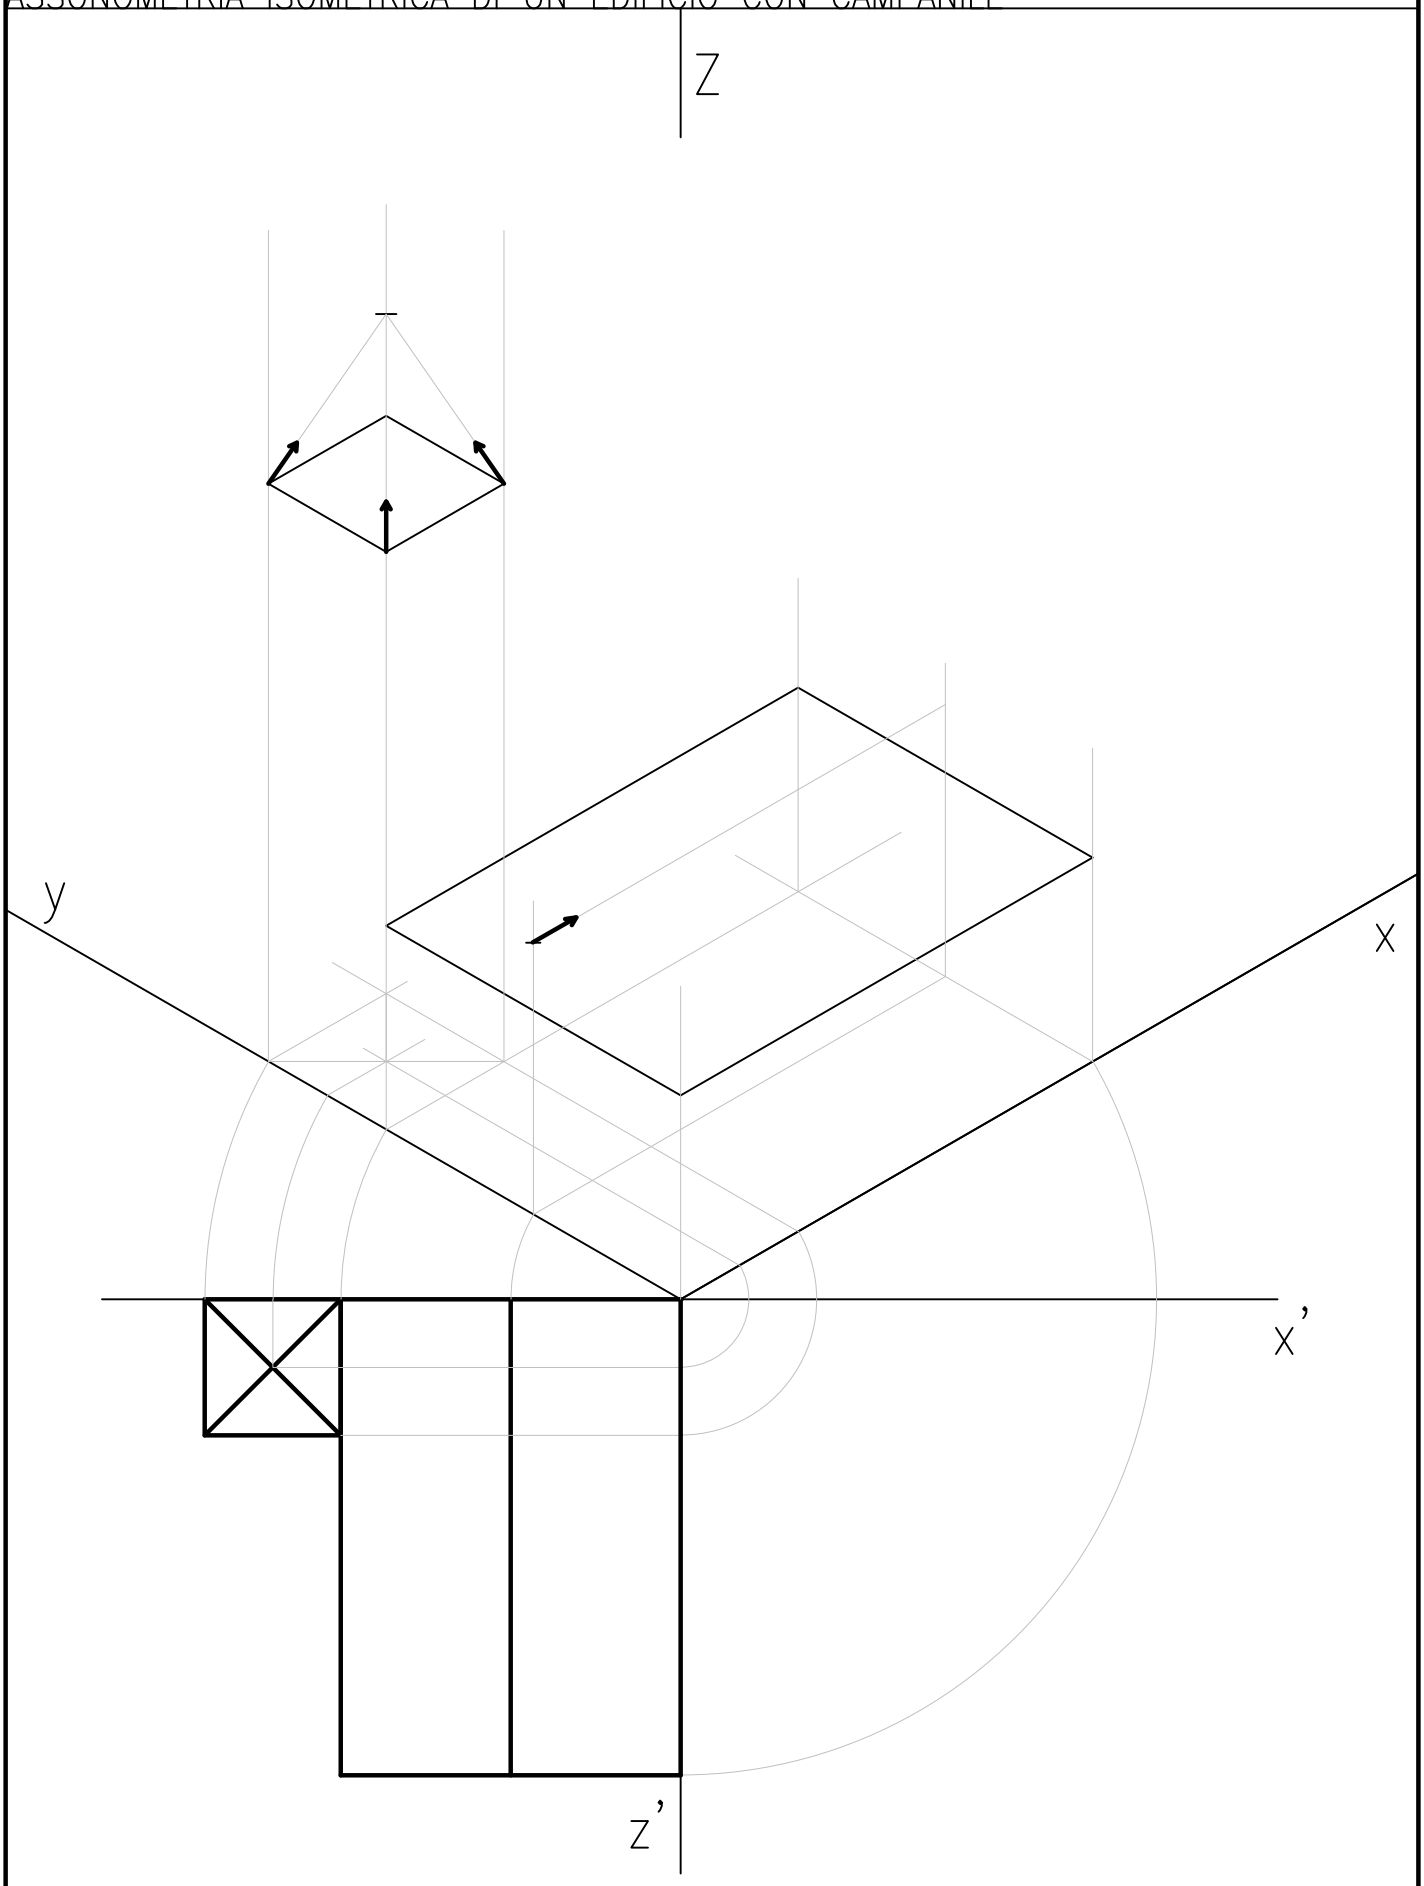

DATA ALUNNO

CLASSE TAVOLA 9

ASSONOMETRIA ISOMETRICA DI UN EDIFICIO CON CAMPANILE

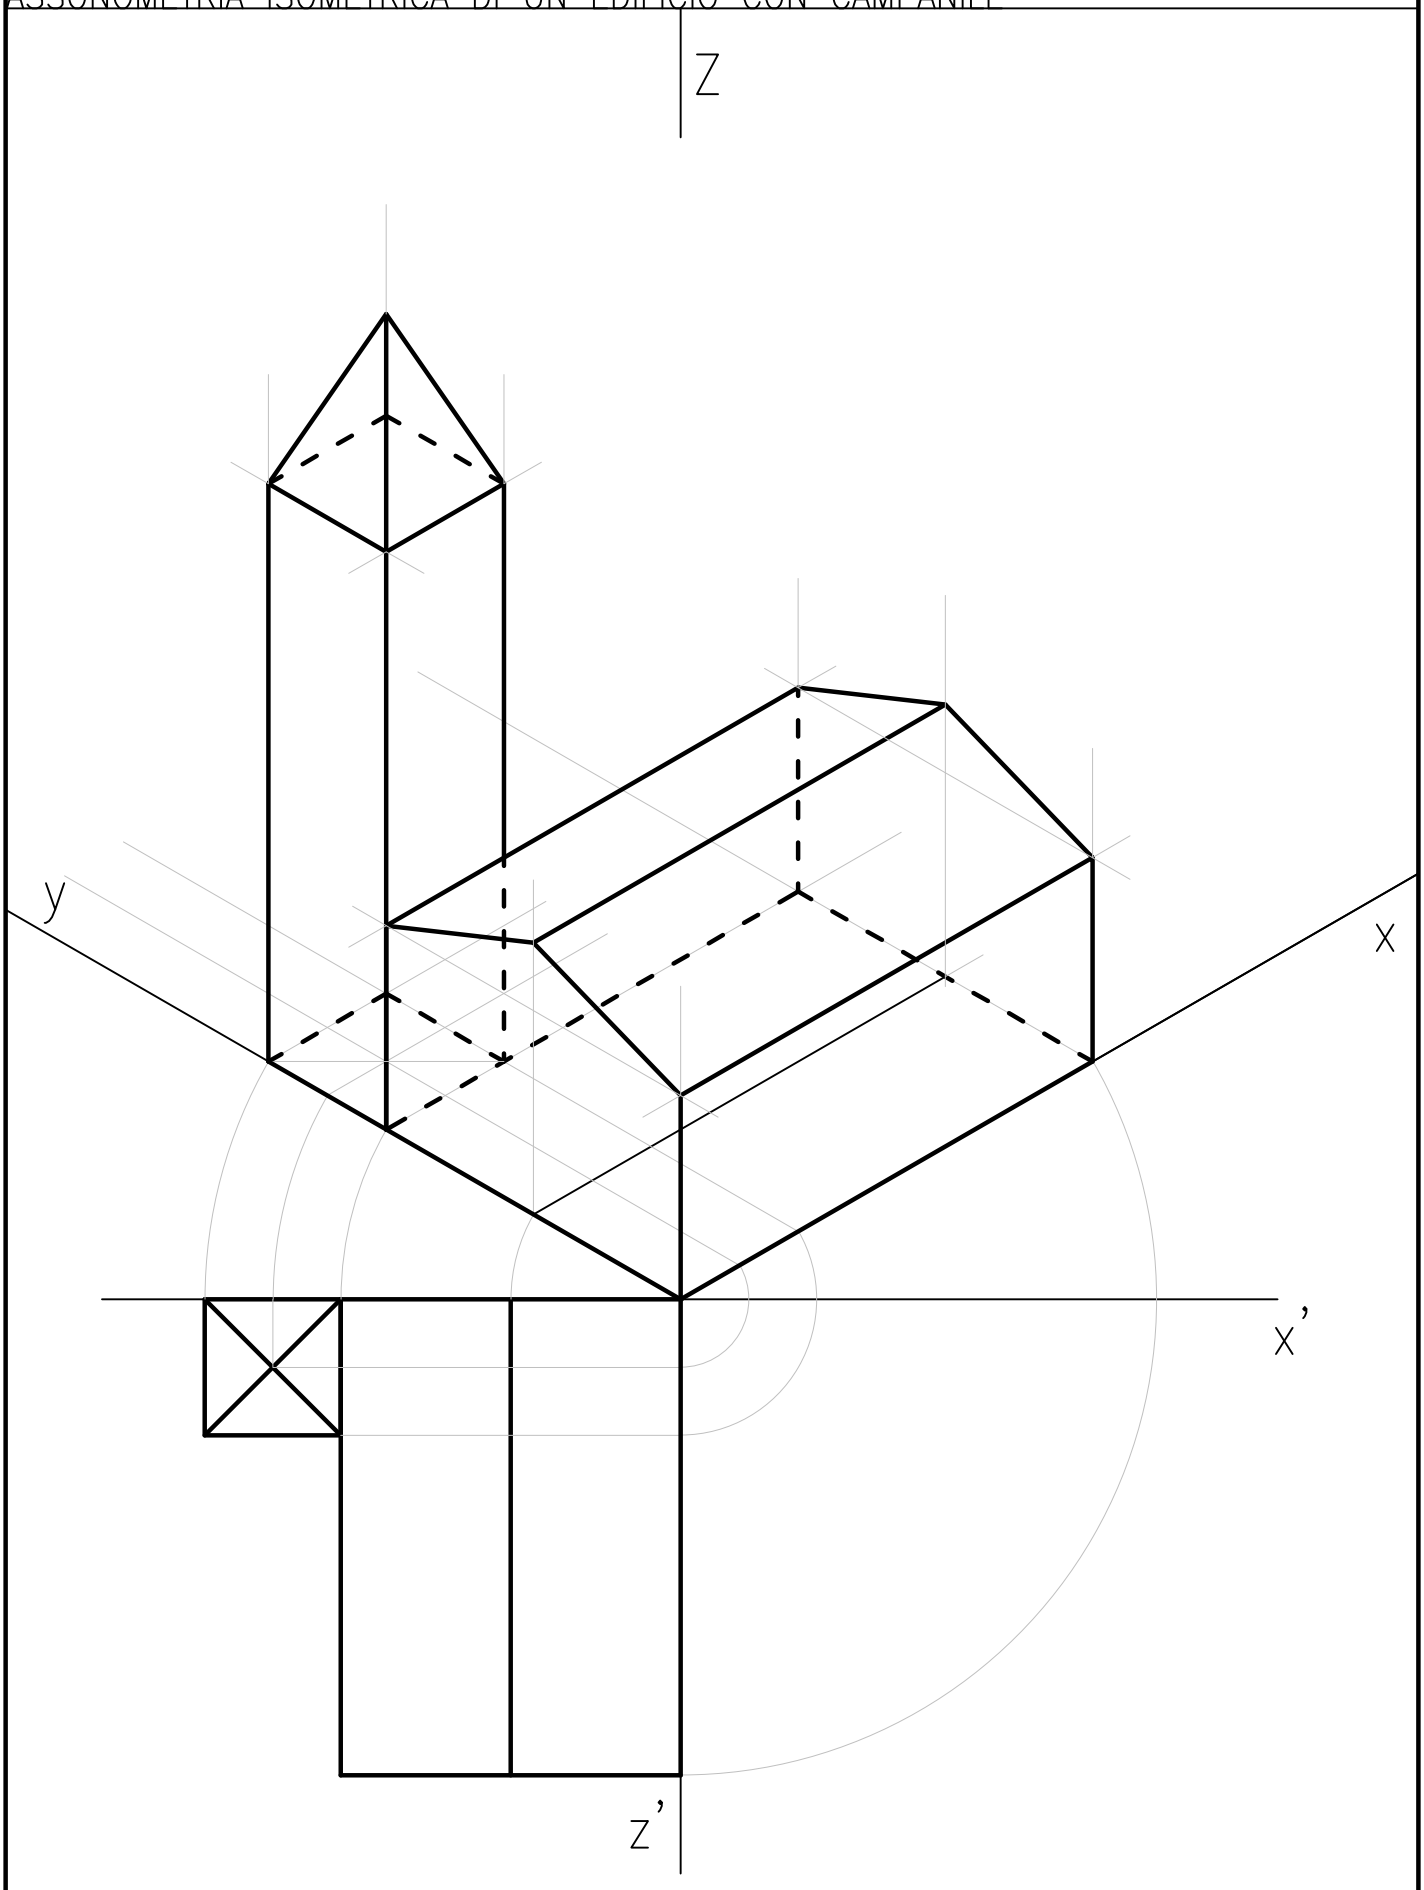

DATA ALUNNO