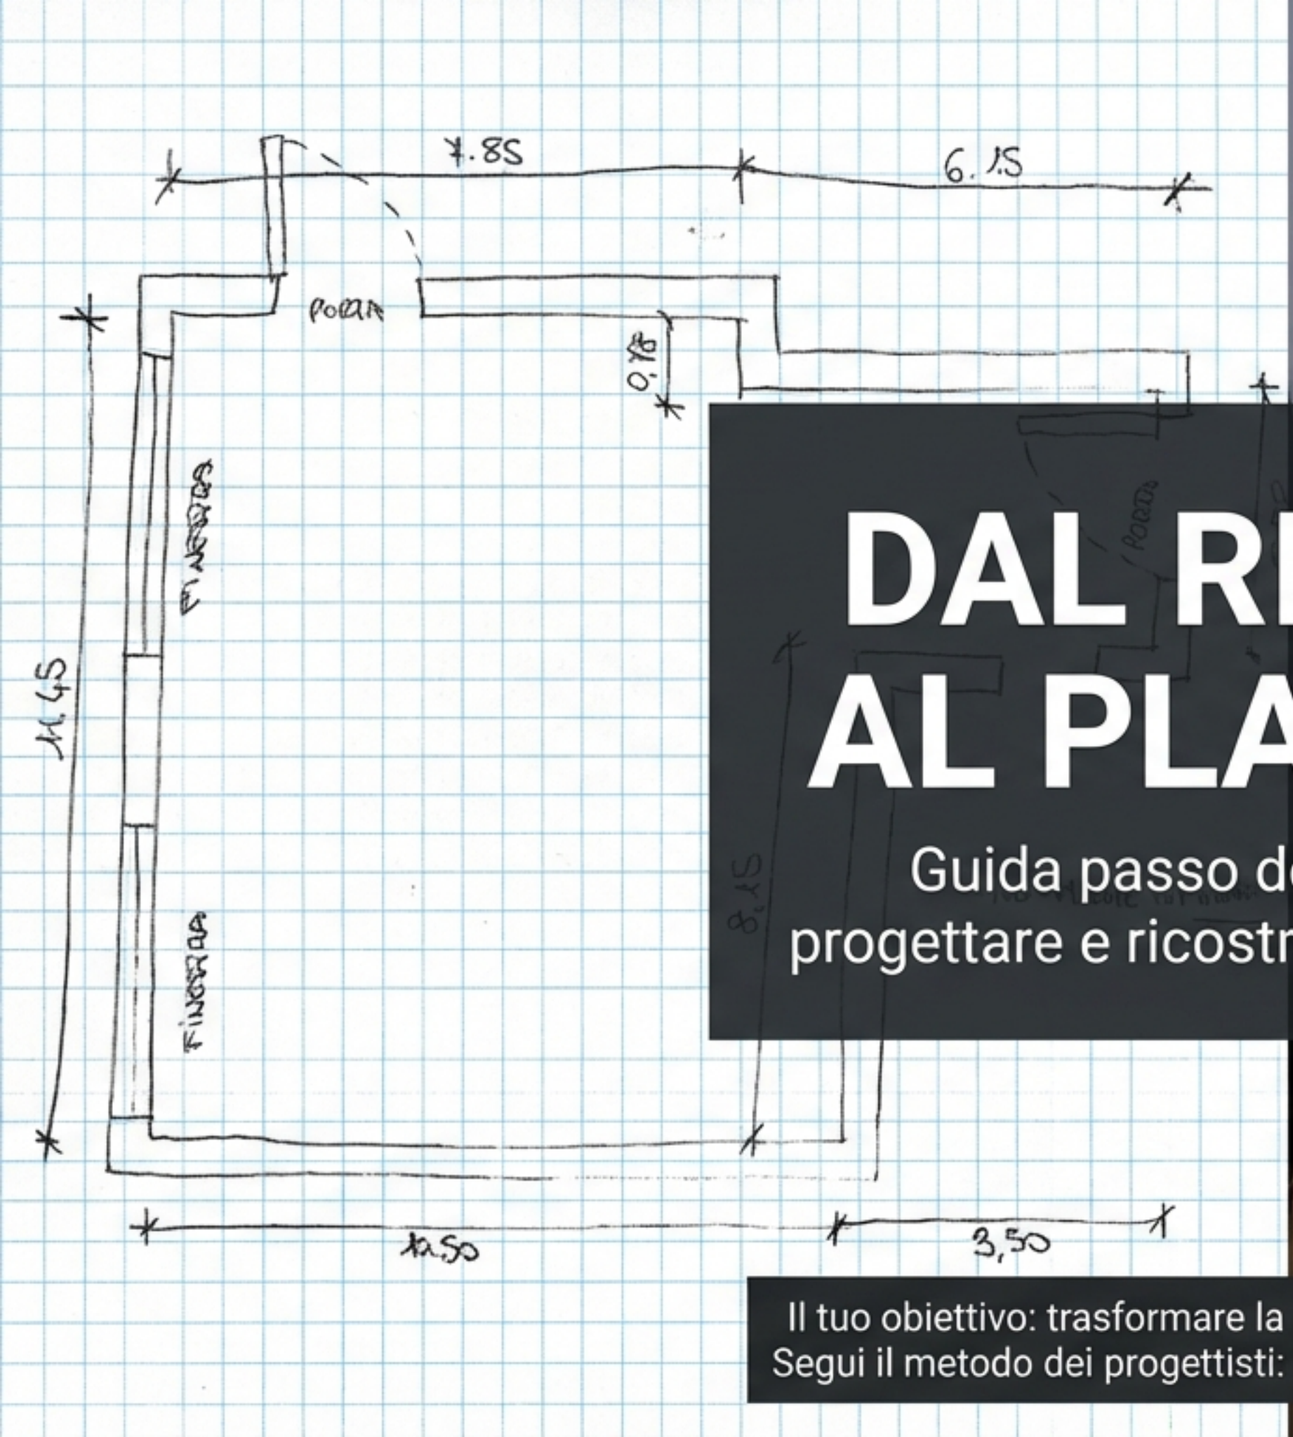


DAL RILIEVO AL PLASTICO

Guida passo dopo passo per progettare e ricostruire la tua camera.

Il tuo obiettivo: trasformare la realtà in un modello in scala.
Segui il metodo dei progettisti: misurare, disegnare, costruire.

NotebookLM

IL CICLO DEL PROGETTO



1. RILIEVO
Raccolta Dati

2. DISEGNO TECNICO
Progettazione in Scala


3. REALIZZAZIONE
Costruzione del Plastico

NotebookLM

FASE 1: RILIEVO IN BOZZA

Strumenti e primi passi.



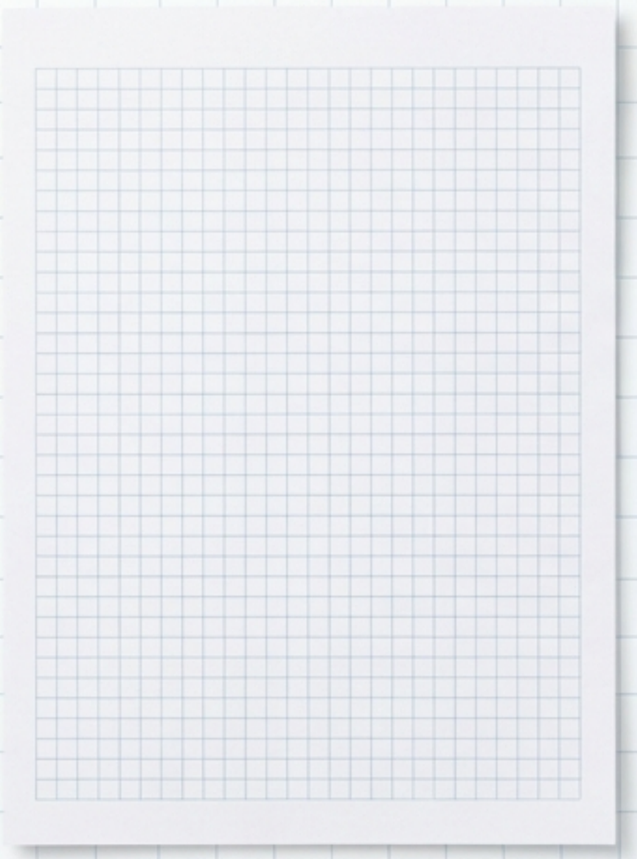


Obiettivo: Fare un "disegno di massima" della pianta (vista dall'alto) rispettando le proporzioni a occhio.

Strumenti: Foglio a quadretti (0,5 cm), matita, gomma, metro flessibile.

Regola d'oro: In questa fase non serve la perfezione grafica, ma la precisione nei numeri.

NotebookLM

COME PRENDERE LE MISURE

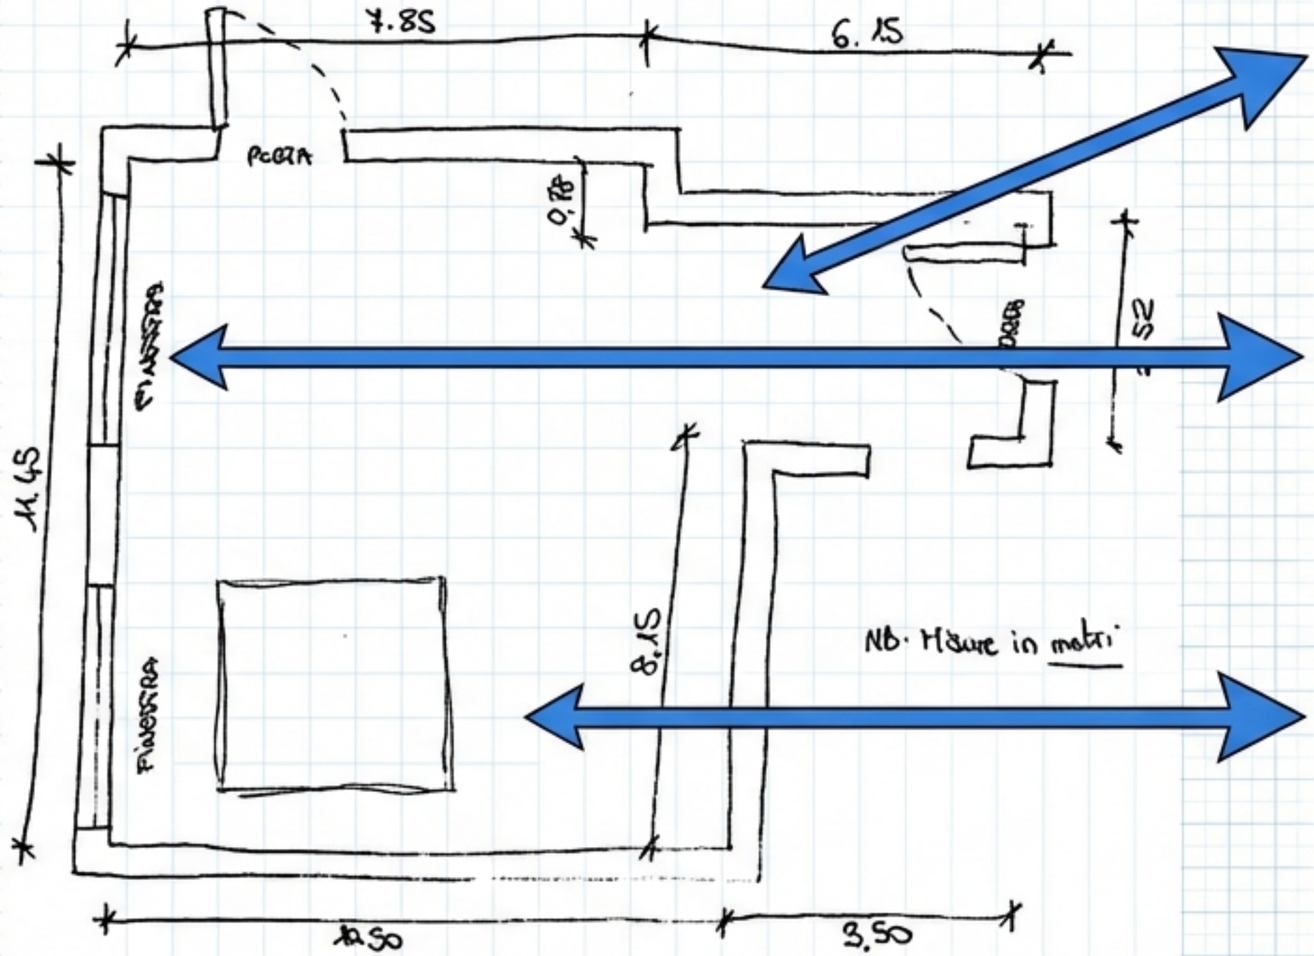

1. Ingombro della stanza
Misura prima i muri perimetrali, comprese eventuali riseghe.

2. Le Aperture
Misura la larghezza di porte e finestre.
Nota: segna a parte le altezze dei parapetti e degli architravi.

3. Gli Arredi
Misura l'ingombro esterno (lunghezza, larghezza, altezza).
Basta il volume.


Attenzione: Scrivi sul foglio le misure **REALI** (in metri o centimetri), **non quelle ridotte.**

NotebookLM

FASE 2: RILIEVO IN BELLA

Tradurre la realtà sul foglio da disegno.

Strumenti di precisione: Foglio da disegno squadrato, matite 2H (dura/sottile) e HB (morbida/spessa), 2 squadrette.
La Scala di Riduzione: Dobbiamo rimpicciolire la stanza per farla entrare nel foglio.
Scelta della Scala: Usa **1:20** (standard) o **1:25** (se la camera è molto grande).
Primo Passo: Traccia gli assi orizzontale e verticale leggeri al centro del foglio.

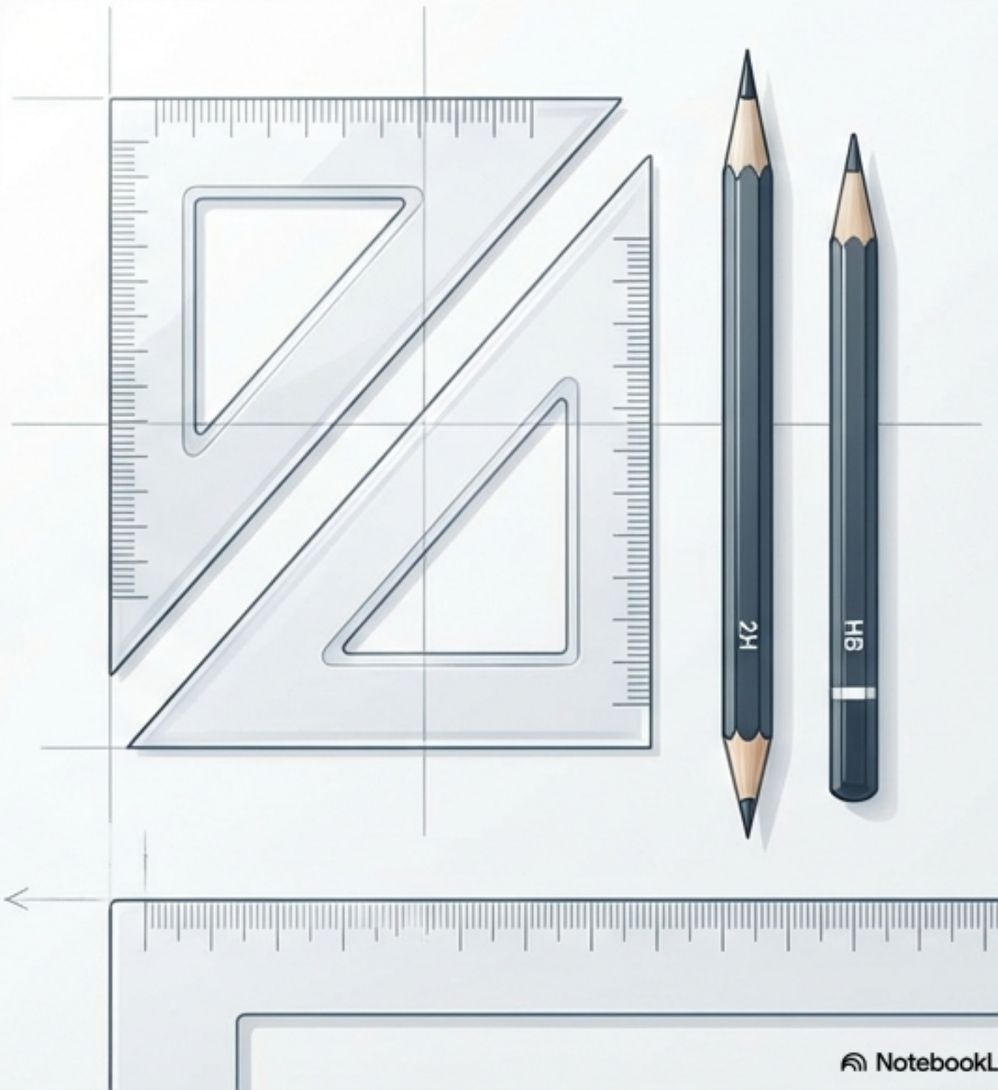

NotebookLM

LA MATEMATICA DELLA SCALA



Esempio Pratico (Scala 1:20)


- Muro reale: **3,00 metri** (300 cm)
- Calcolo: **300 : 20 = 15 cm**
- Sul foglio disegnerai una linea di **15 cm**.

Procedimento: Calcola l'ingombro totale del pavimento e disegna il rettangolo di base centrato sugli assi.

NotebookLM

DISEGNARE LE MURATURE

Creazione dei Muri Esterni ed Interni

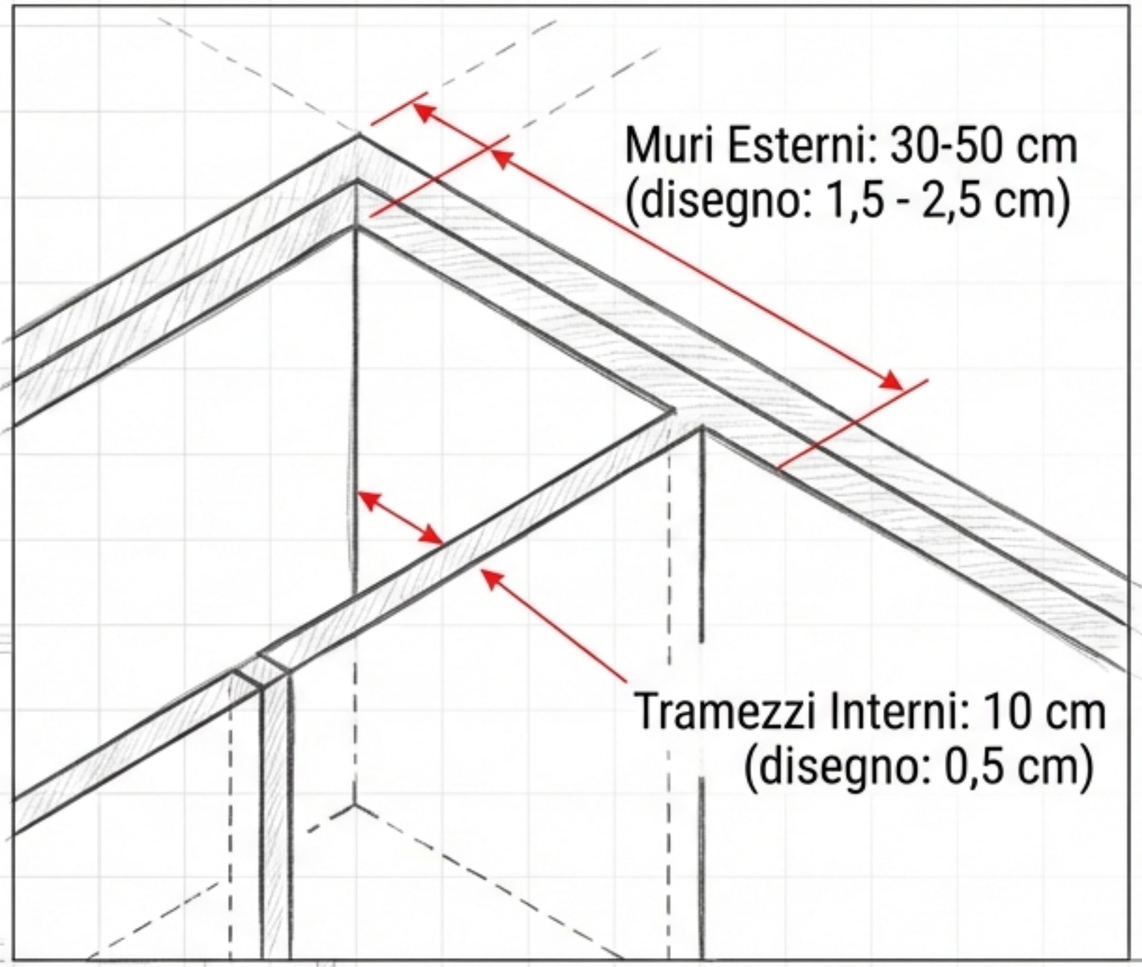

- **Spessori:** Dal rettangolo del pavimento, disegna lo spessore dei muri verso l'esterno.
- **Linee:** Usa la matita **2H** (leggera) per la costruzione. Ripassa con la matita **HB** (più scura) solo i muri sezionati.



NotebookLM

APERTURE E ARREDI



Porta e senso di apertura



Ingombro Arredo

Porte e Finestre: Riporta la larghezza delle aperture nelle posizioni rilevate.

Arredi: Procedi con il disegno dei mobili all'interno della stanza.

Tecnica: Usa un tratto molto sottile (**matita 2H**). Disegna solo l'ingombro (rettangoli), senza dettagli decorativi per ora.


Quote: Aggiungi le quote principali (le misure) all'esterno del disegno.

NotebookLM

1


In un foglio da disegno
disegnare la squadratura
e gli assi

2

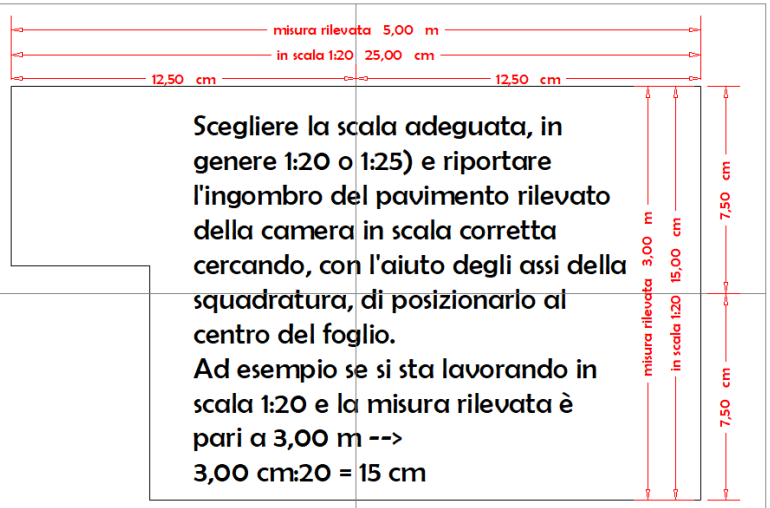

Scegliere la scala adeguata, in genere 1:20 o 1:25) e riportare l'ingombro del pavimento rilevato della camera in scala corretta cercando, con l'aiuto degli assi della squadratura, di posizionarlo al centro del foglio.
Ad esempio se si sta lavorando in scala 1:20 e la misura rilevata è pari a 3,00 m -->
3,00 cm:20 = 15 cm

3

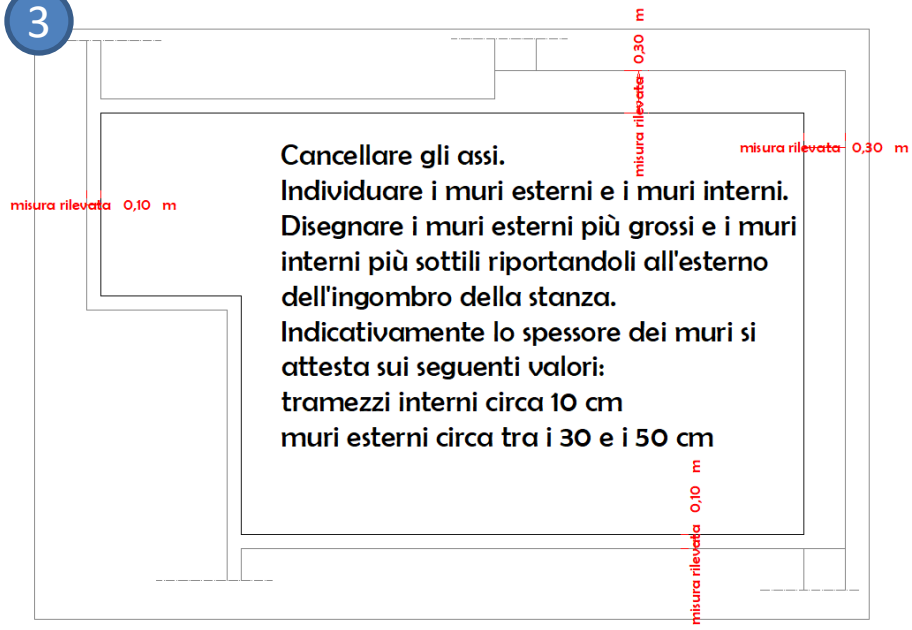

Cancellare gli assi.
Individuare i muri esterni e i muri interni.
Disegnare i muri esterni più grossi e i muri interni più sottili riportandoli all'esterno dell'ingombro della stanza.
Indicativamente lo spessore dei muri si attesta sui seguenti valori:
tramezzi interni circa 10 cm
muri esterni circa tra i 30 e i 50 cm

4



Riportare sui muri e in scala le larghezze degli infissi, (porte e finestre), nelle posizioni rilevate disegnandoli graficamente come spiegato a lezione

5


Ripassare con la matita HB i muri "sezionati" in modo da metterli in risalto


6


Procedere con il disegno degli arredi della camera da letto, sempre in scala, e con tratto molto sottile (matita 2H).

7


Prospetto 1
Prospetto 4b
Prospetto 3b
Prospetto 2
Prospetto 4a
Prospetto 3a
Per costruire il modellino in cartoncino prosegui "ribaltando" su altri fogli da disegno i prospetti interni delle pareti della camera riportando almeno i muri e gli infissi, (porte e finestre).


8

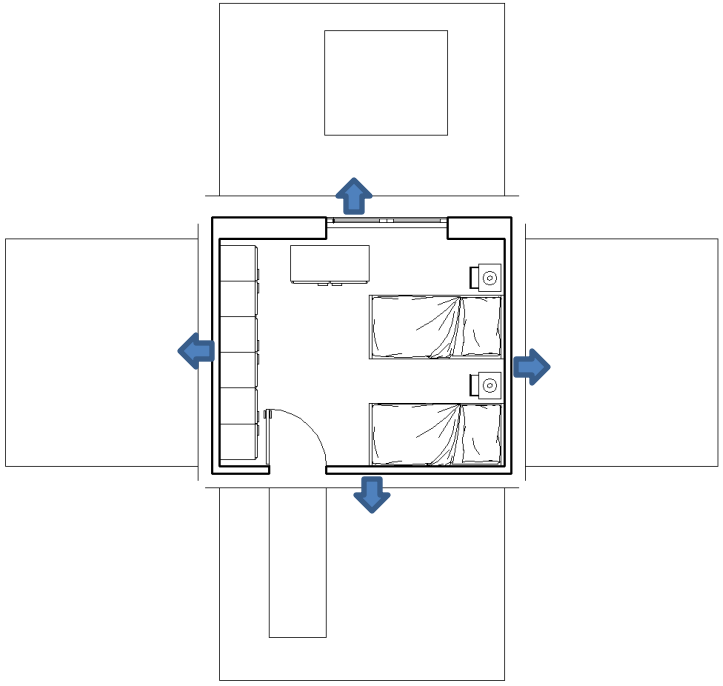

PREPARAZIONE AL PLASTICO: I PROSPETTI

Il Concetto:
Per costruire il modello, dobbiamo disegnare le pareti in alzato (vista frontale).


Ribaltamento:
Immagina di “ribaltare” i prospetti delle pareti sui lati della pianta.

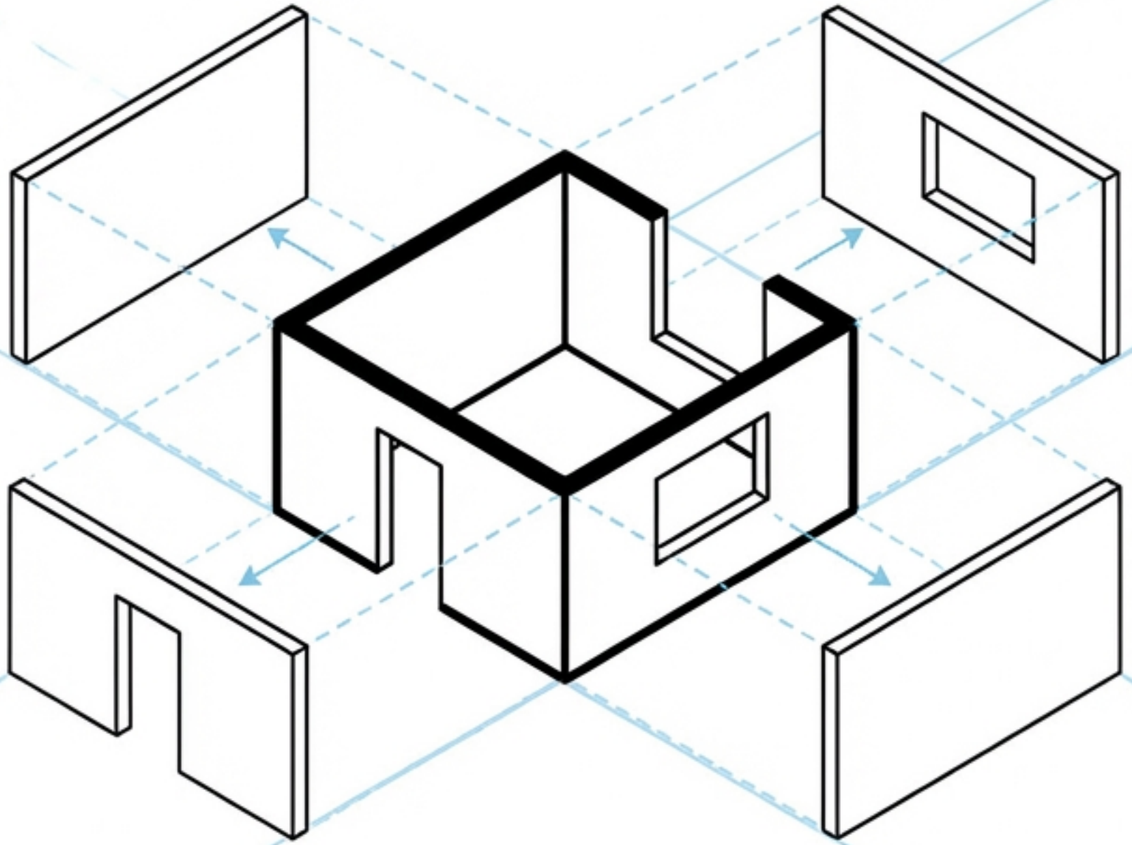

Dati necessari:
Usa le misure orizzontali dalla tua pianta e le **altezze** (finestre, porte, soffitto) che avevi annotato nella Fase 1.

NotebookLM

Esempio camera da letto arredata con ribaltamenti pareti arredate.

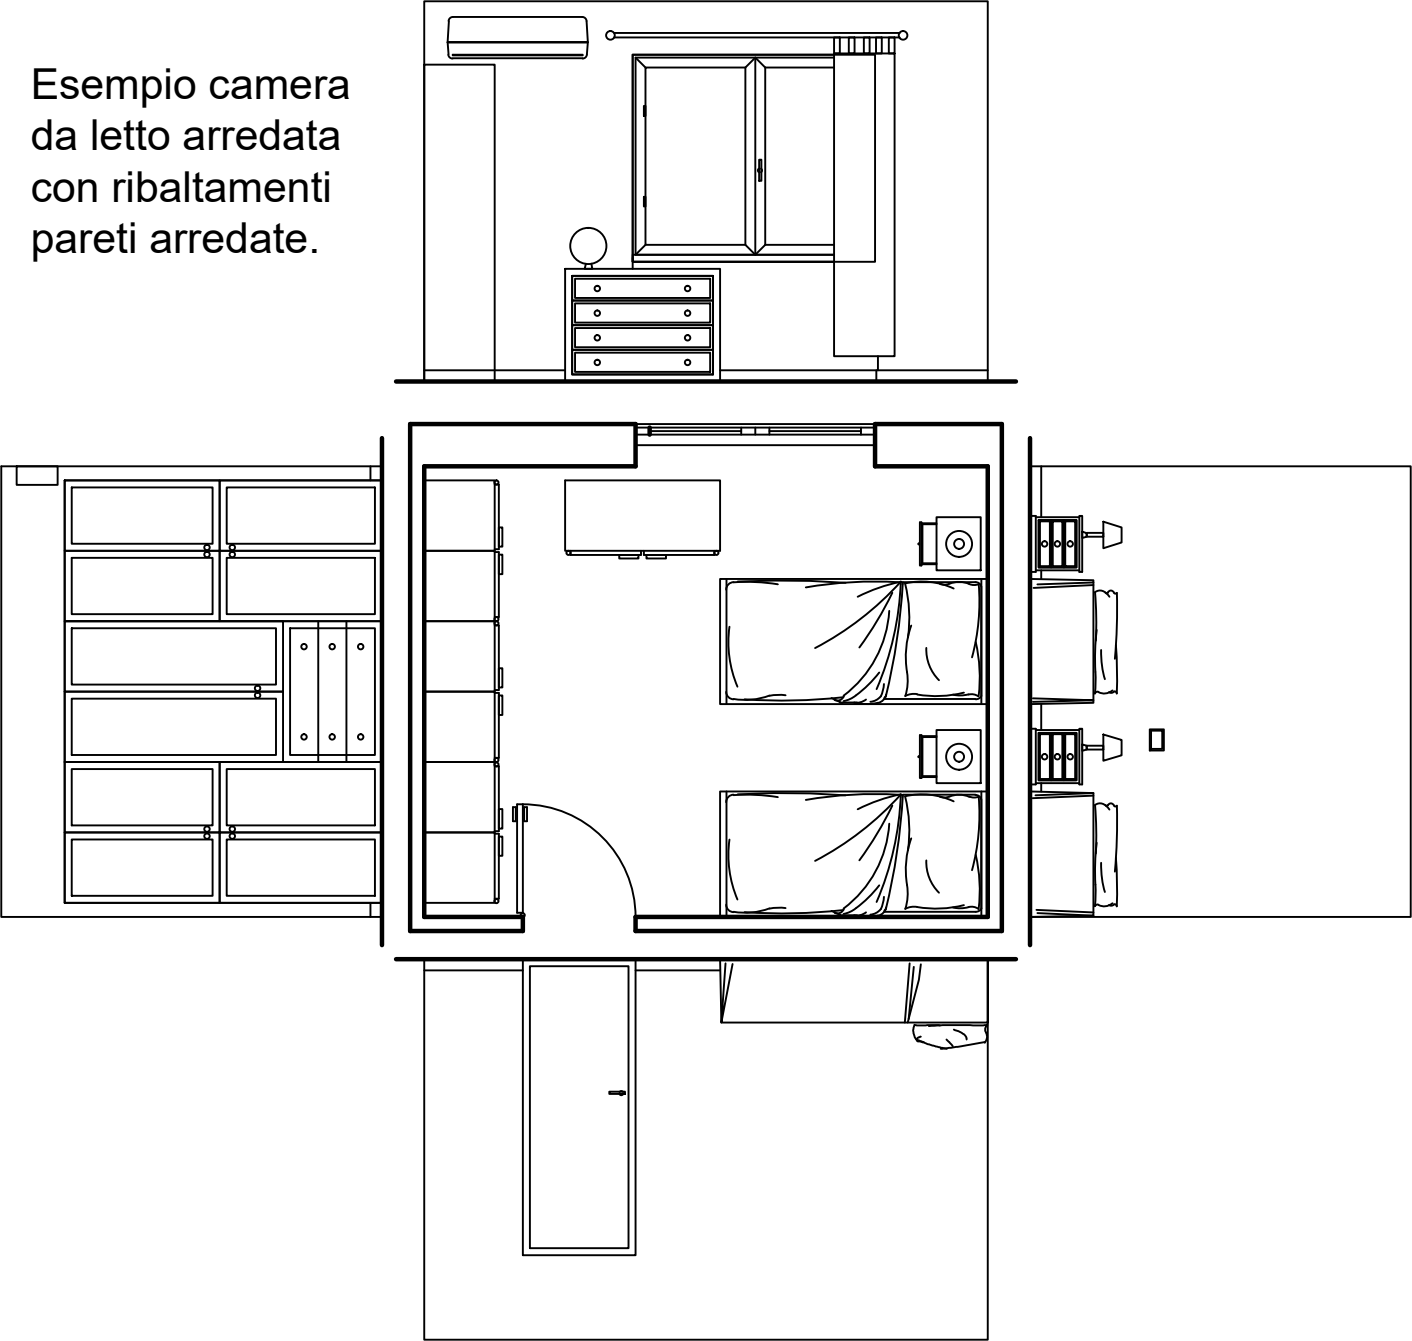

FASE 3: REALIZZAZIONE IN CARTONCINO


Materiali e taglio.

Materiali: Cartoncino (o una scatola di scarpe), forbici, colla/nastro adesivo.

•**Trasferimento:** Riporta il disegno delle pareti sul cartoncino usando le squadrette.

•**Il Taglio:** Ritaglia la pianta e le pareti.

•**Importante:** Ritaglia le finestre e le porte ***prima*** di incollare le pareti. Per le finestre, puoi tagliare **solo 3 lati per creare l'effetto ante aperte**.

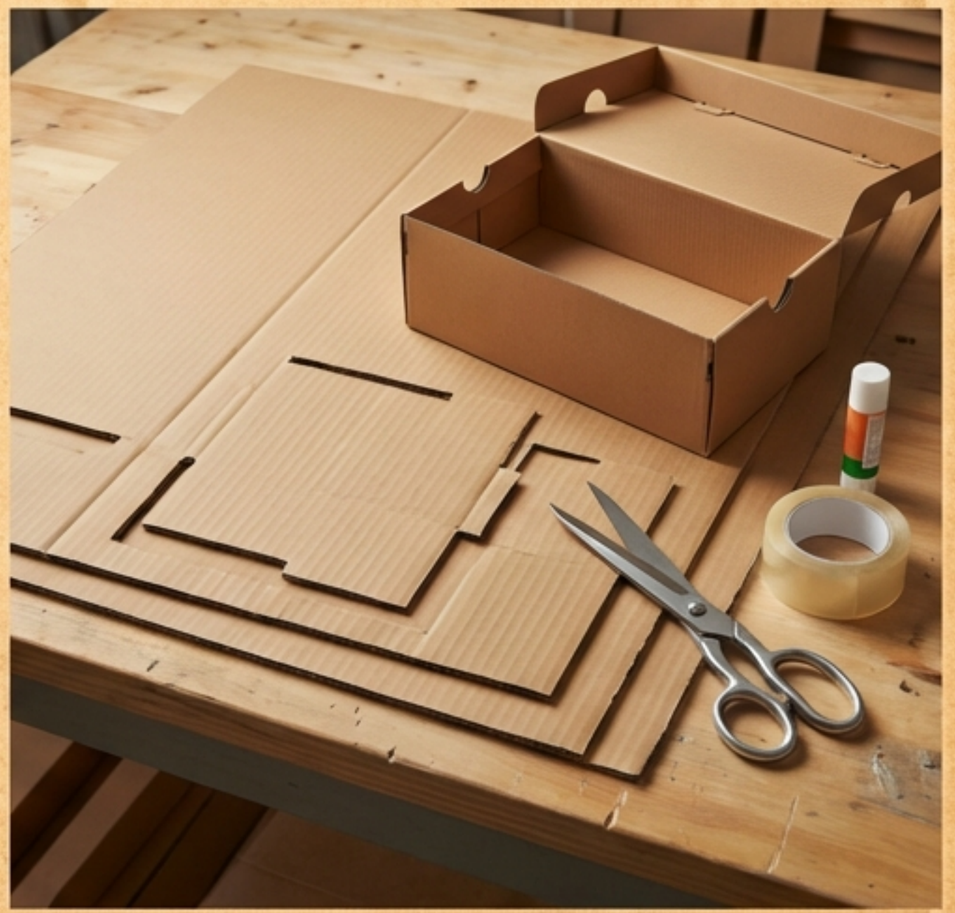

NotebookLM

ASSEMBLAGGIO DELLA STANZA

- **Costruzione:** Incolla le pareti **verticalmente lungo il perimetro del pavimento.**
- **Struttura:** Usa nastro adesivo trasparente o colla (vinavil/colla a caldo) per fissare gli angoli.
- **Consiglio da Pro:** Lascia una parete "rimovibile" o non incollarla affatto. Questo permetterà di vedere meglio l'interno e gli arredi una volta finito.



NotebookLM


COSTRUIRE GLI ARREDI





- **Sviluppo dei Solidi**: I mobili sono semplici parallelepipedi. Disegna lo sviluppo piano (la "rete") sul cartoncino.
- **Dettagli Grafici**: Disegna cassetti, maniglie e dettagli sul cartoncino *prima* di piegarlo.
- **Montaggio**: Piega lungo le linee e chiudi i volumi con la colla.
- **Esempi**: Letto, armadio, scrivania, comodino.

NotebookLM


Esempio letto, comodino, cassettiera

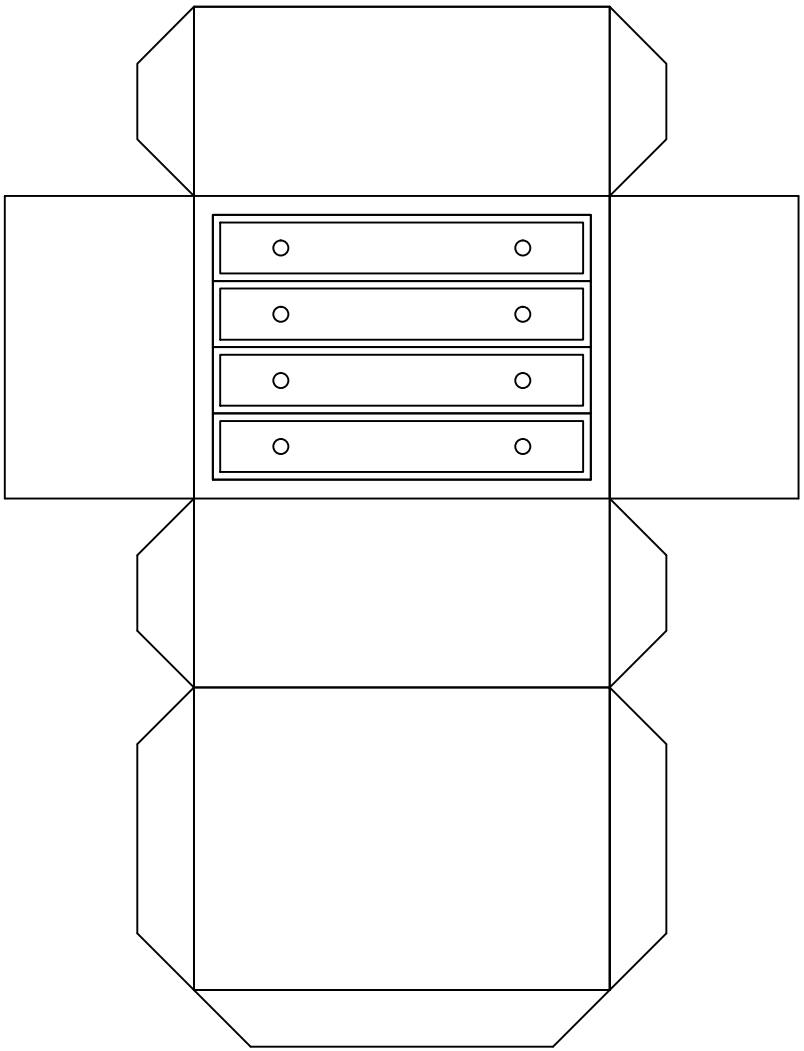

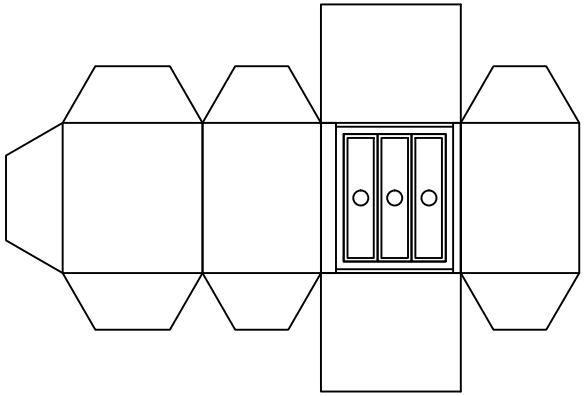

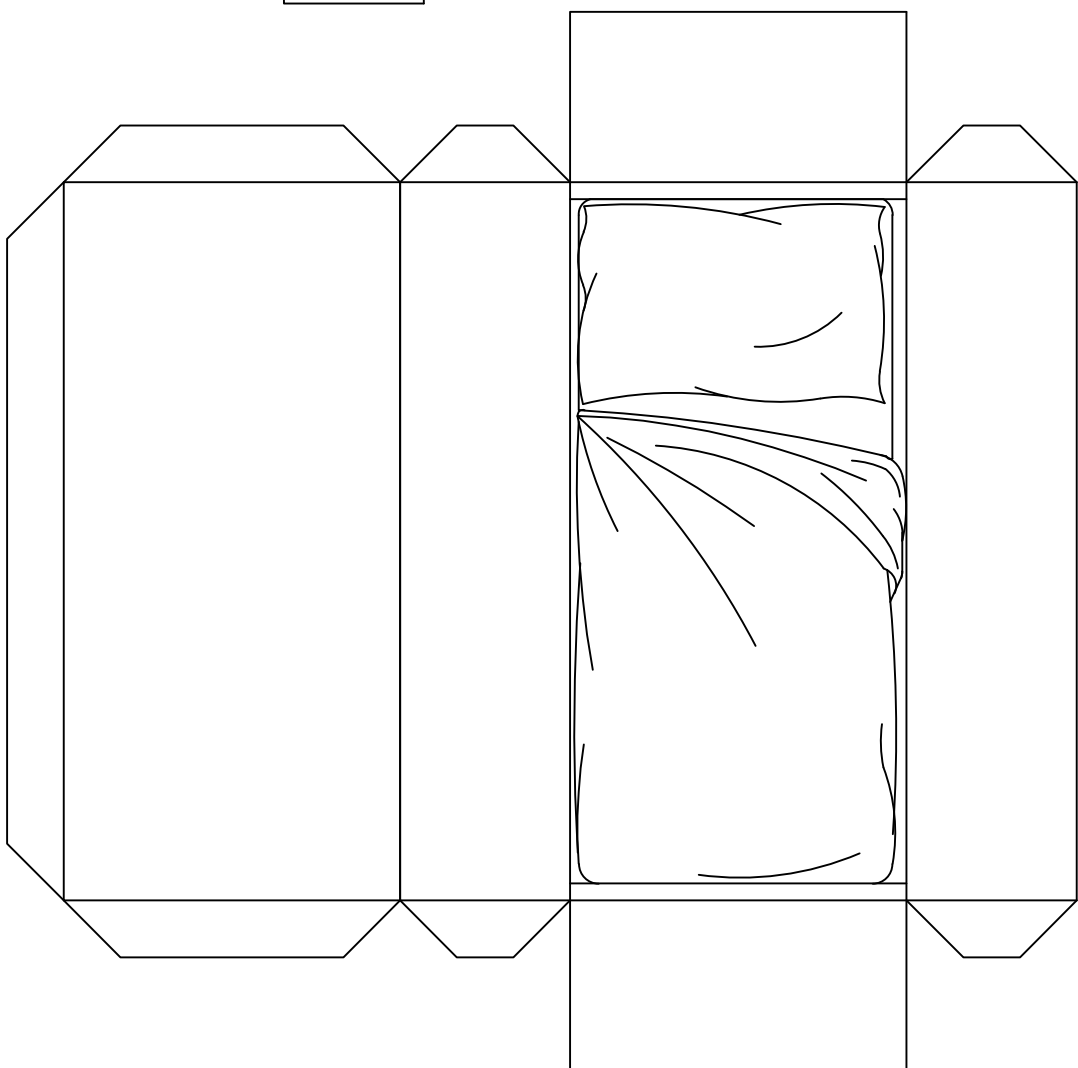


Esempio guardaroba

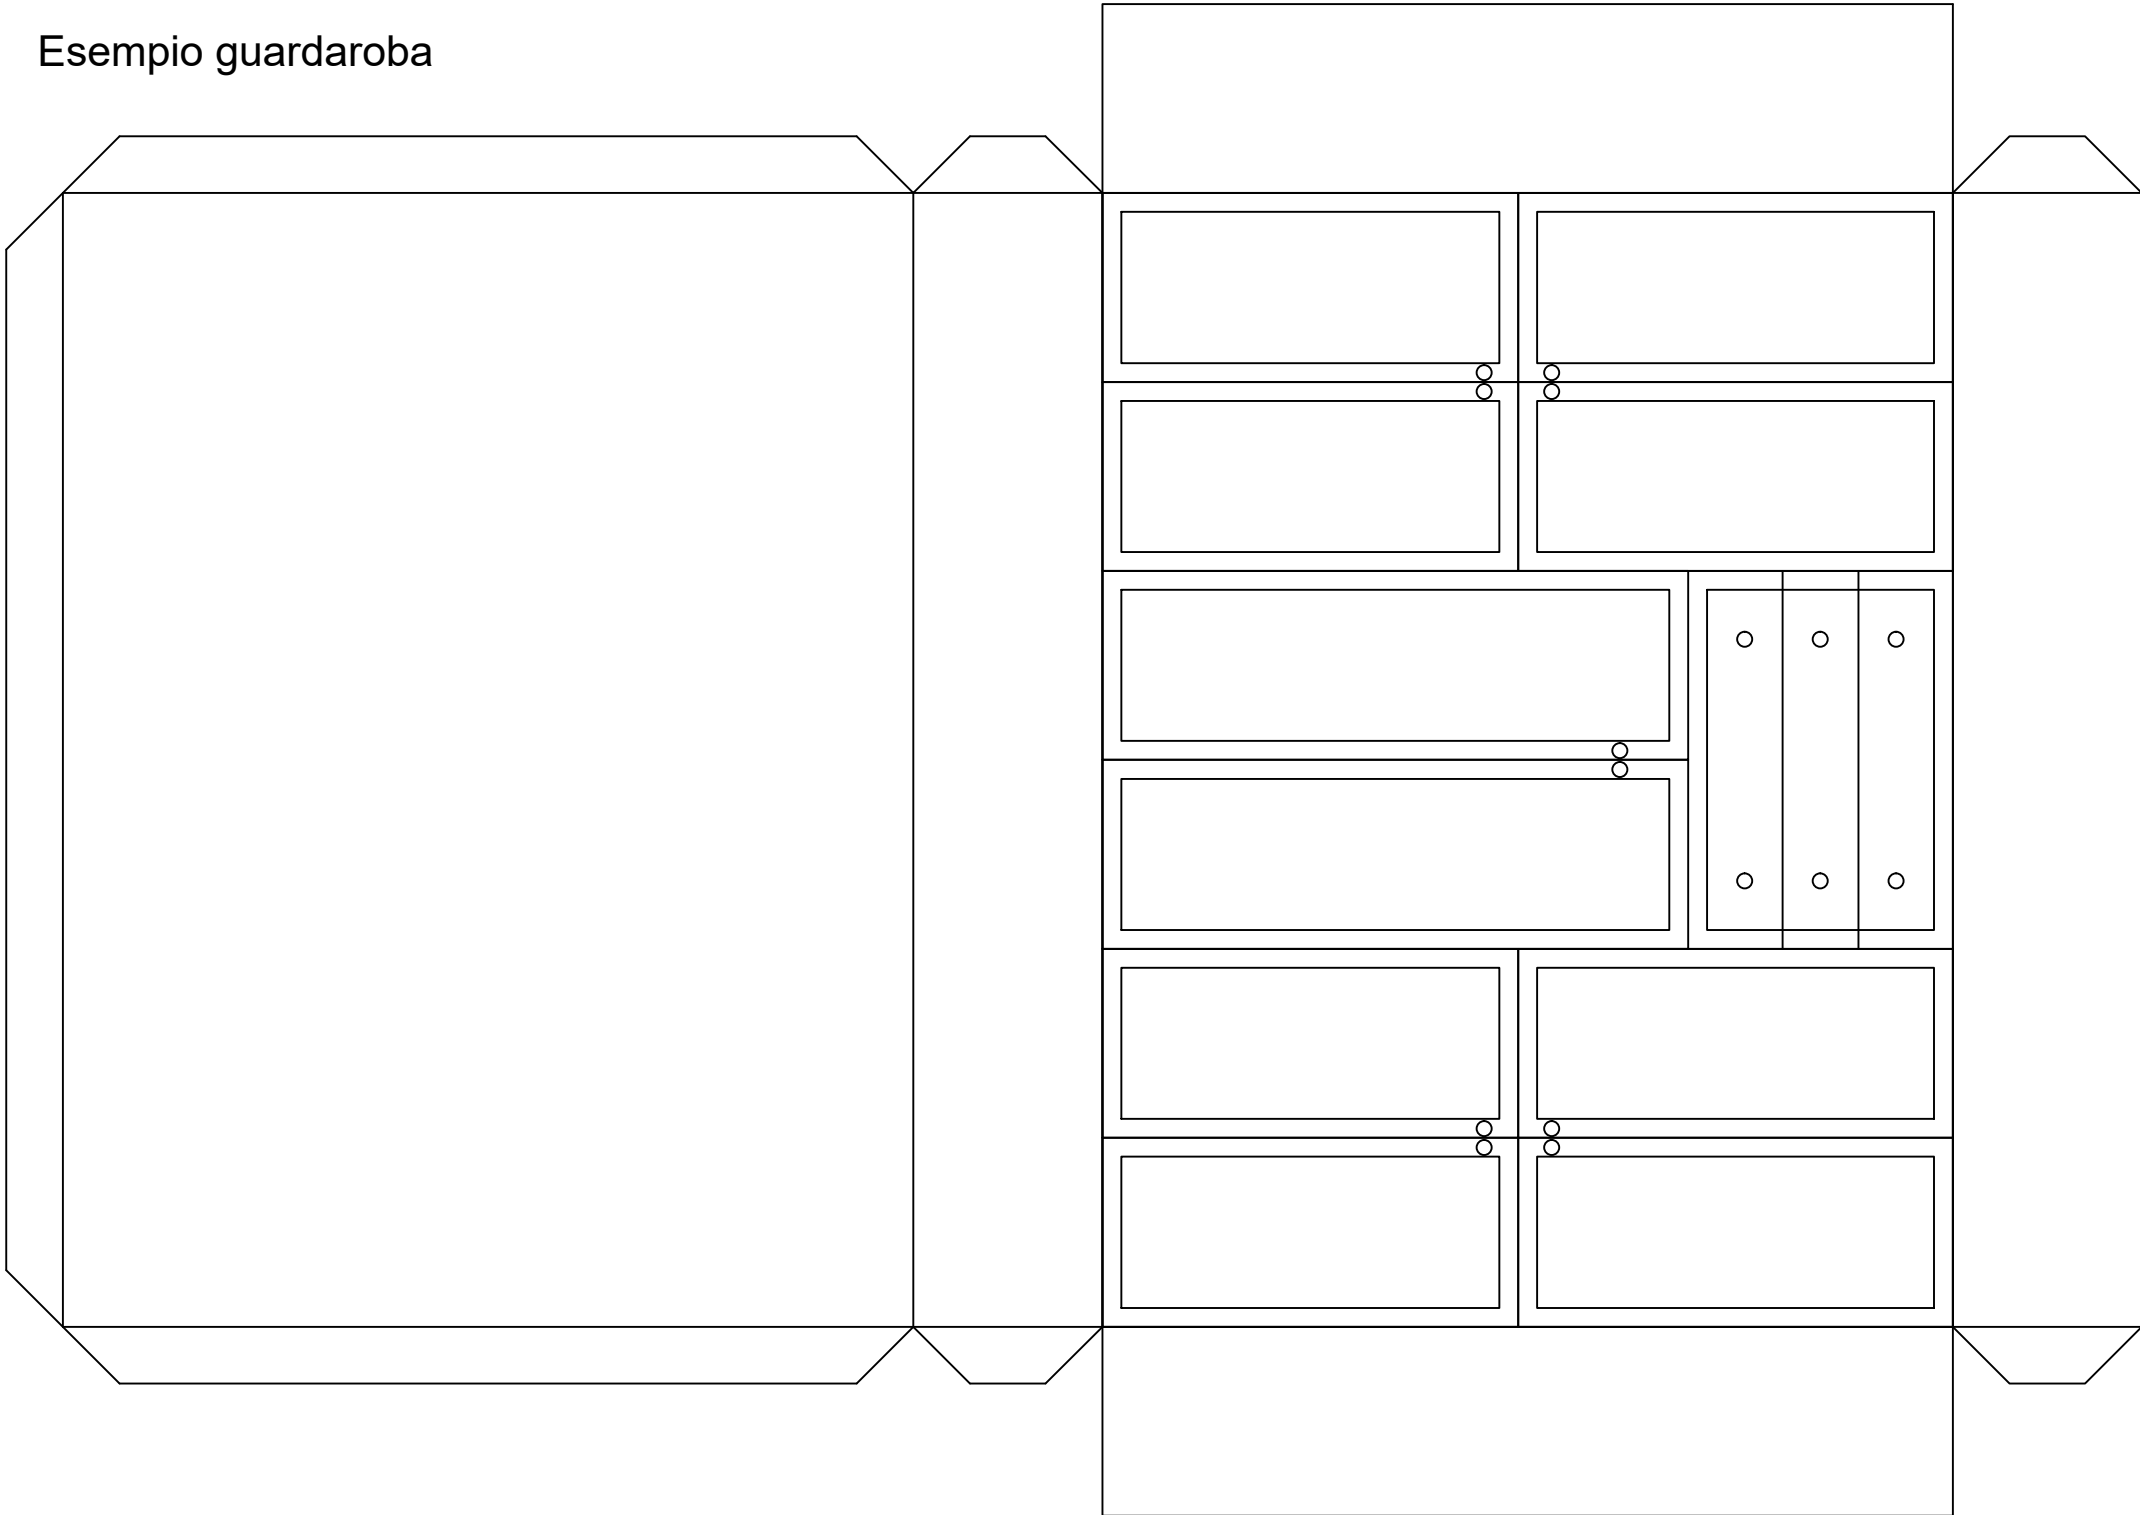

FINITURE E CREATIVITÀ



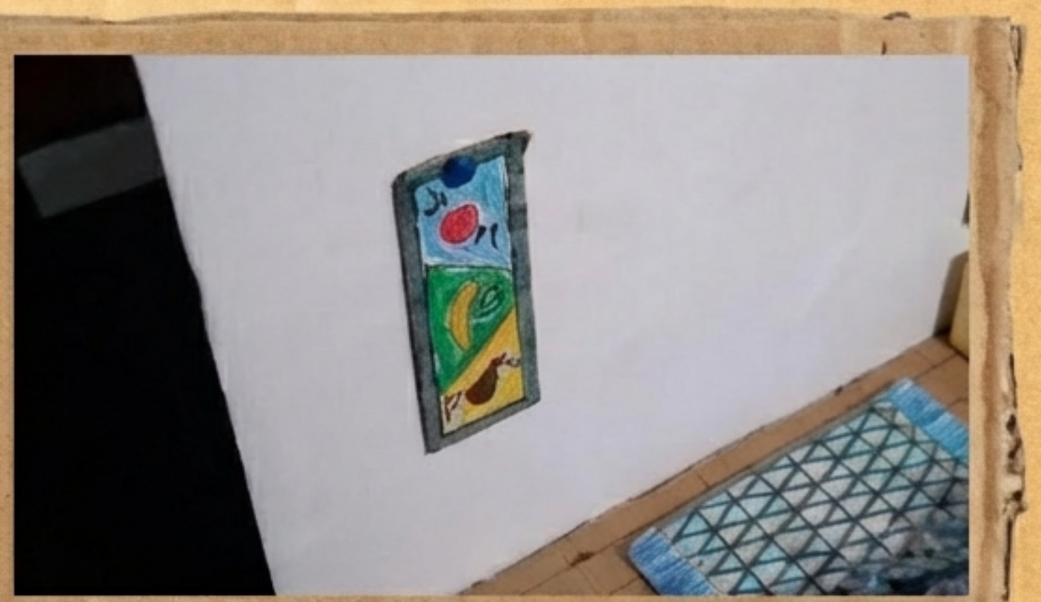

- **Personalizzazione:** Rendi la stanza vissuta e realistica.
- **Materiali di Riciclo:** Pezzi di stoffa per lenzuola, coperte e tappeti. Ritagli di carta colorata per quadri e poster.
- **Pavimento:** Puoi disegnare le piastrelle o il parquet direttamente sulla base prima di incollare i mobili.

NotebookLM

GALLERIA DI ISPIRAZIONE







Osserva come i colori e i piccoli dettagli (un computer di carta, un quadro alla parete) fanno la differenza. Il tuo modello racconta la storia del tuo spazio.

NotebookLM





"La cameretta" di Van Gogh - Il modellino di Amelia



CHECKLIST FINALE

- ☐ **Scala Corretta**: Le proporzioni corrispondono alla realtà?
- ☐ **Verticalità**: I muri sono dritti e perpendicolari al pavimento?
- ☐ **Completezza**: Ci sono tutti gli arredi principali?
- ☐ **Pulizia**: Il modello è ordinato e senza eccessi di colla?

Ottimo lavoro! Ora sei pronto a presentare il tuo progetto.

NotebookLM