CLASSE TAVOLA

TRILITE

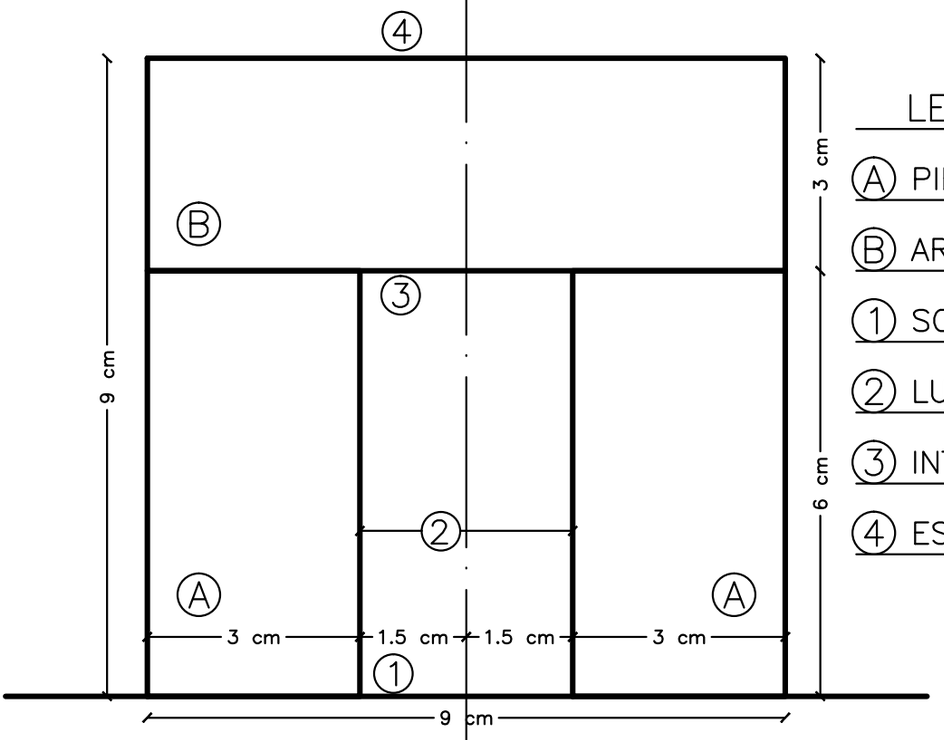

LEGENDA

Ⓐ PIEDRITTO

Ⓑ ARCHITRAVE

① SOGLIA

② LUCE

③ INTRADOSSO

④ ESTRADOSSO

ARCO A TUTTO SESTO

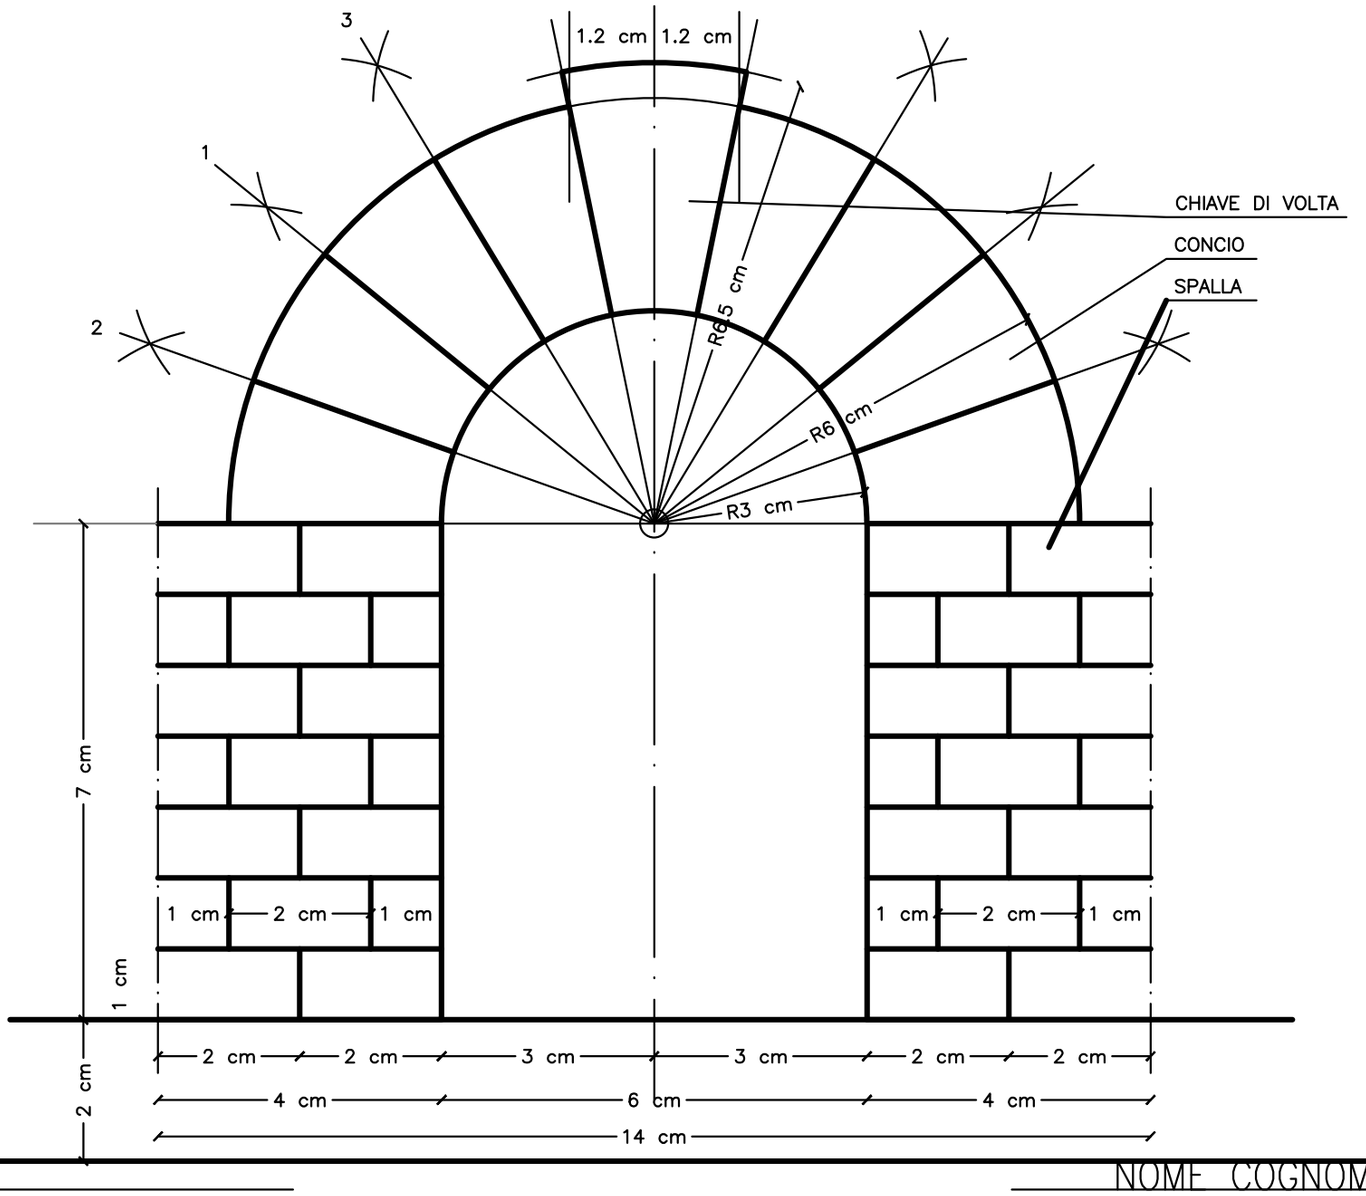

DATA NOME COGNOME

CAPRIATA – SCALA 1:25

LEGENDA

Ⓐ PUNTONE 24xh30 cm

Ⓑ CATENA 24xh30 cm

Ⓒ MONACO 24xh30 cm

Ⓓ SAETTONE 24xh30 cm

① ARCARECCIO

② TAVOLATO

③ COPPI

30 cm

24 cm
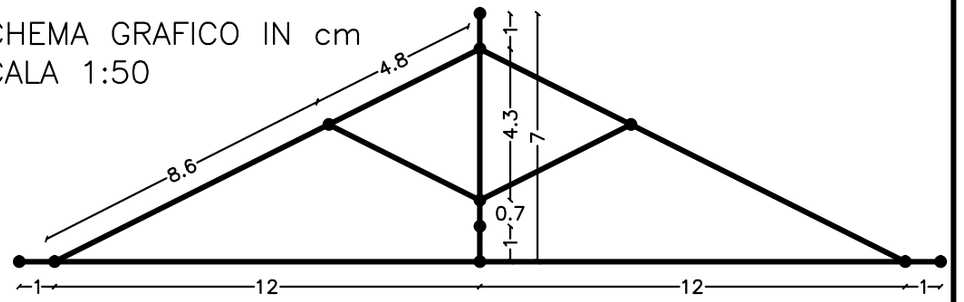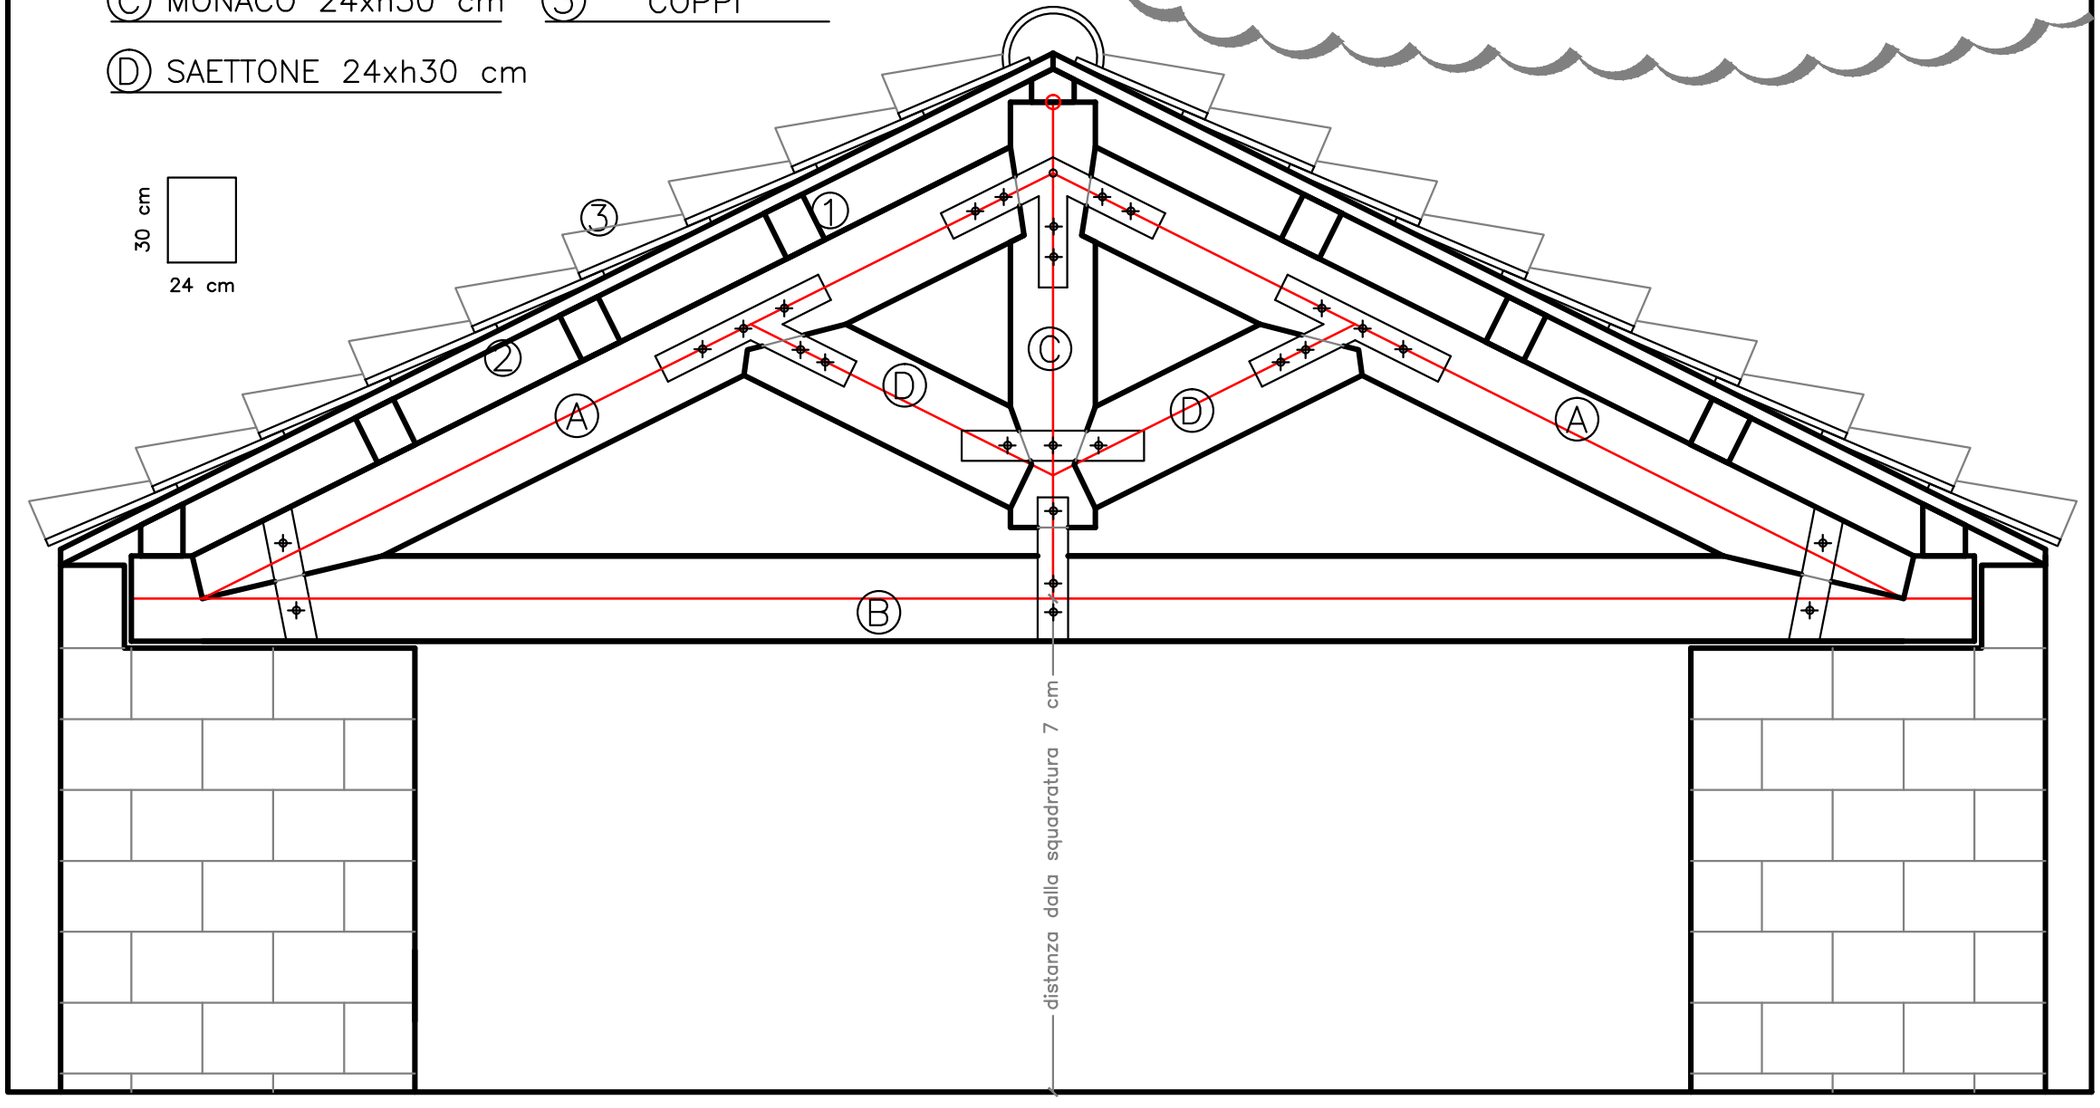
SCHEMA GRAFICO IN cm
SCALA 1:50